

# PROPOSED RESIDENTIAL DEVELOPMENT

FOR

**ADEGBITE USMAN  
OLALEKAN**

AT NO. 8B DUALA STREET, CROWN ESTATE,  
SANGOTEDO, ETI-OSA LOCAL GOVERNMENT AREA  
LAGOS STATE.

PREPARED BY

**YUNGOLA SERVICES LTD.**

(ARCHITECTURAL DESIGN, STRUCTURAL DESIGN, BUILDING  
DEVELOPMENT, PLANNER, SUPERVISION

ADDRESS;

NO 2 OSHOGBO STREET, OGUDU,  
LAGOS STATE


*J&L* ;

08054178584, 07062539641

*DESIGN* ;

AUGUST, 2024.

NOTE:

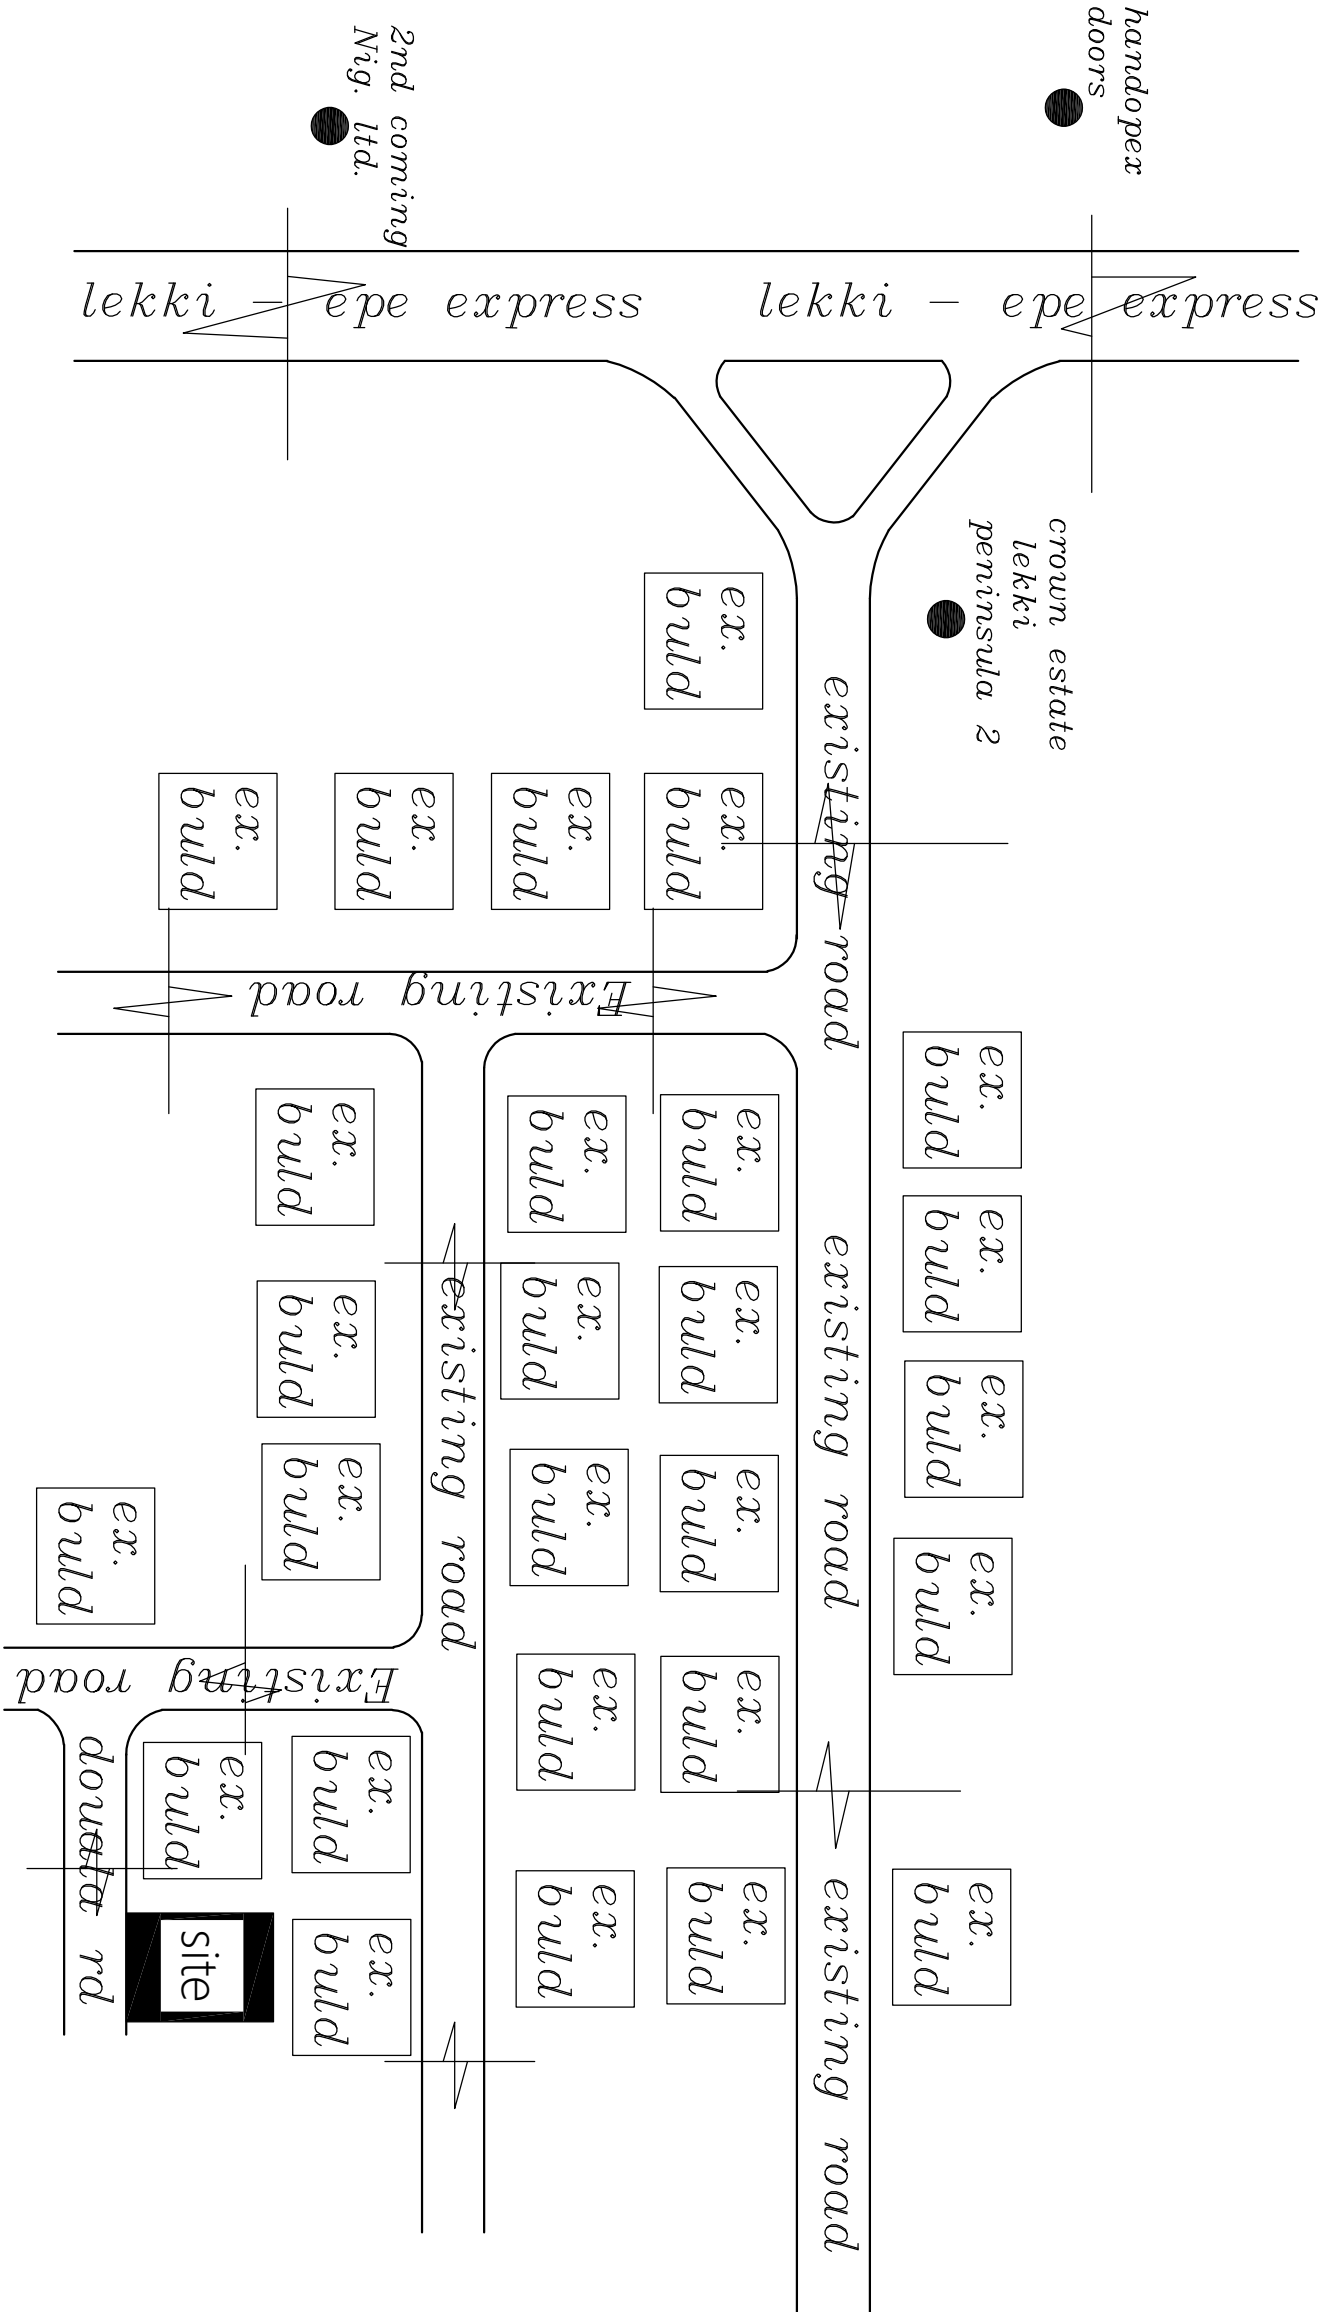

# LOCATION MAP

## general note

- 1) The contractor is to check all the drawing before commencing work.
- 2) Any discrepancies observed on this drawing issued by any other party are to be immediately brought to consultant Architect Notice.
- 3) All dimension are in millimeter.
- 4) Dimension are to be confirmed on site.

## Client :-

ADEGBITE USMAN  
OLALEKAN

## Location :-

AT NO. 8B DUALA STREET, CROWN  
ESTATE, SANGOTEDO, ETI-OSA LOCAL  
GOVERNMENT AREA  
LAGOS STATE.

## Project Title :-

Proposed Residential  
Development

## Architech :-

YUNGOLA SERVICES  
LTD. *Re.1783703*

(ARCHITECTURAL DESIGN,  
STRUCTURAL DESIGN,  
BUILDING DEVELOPMENT,  
PLANNER, SUPERVISION

## OFFICE ADDRESS:

NO 2 OSHOGBO STREET, OGUDU,  
LAGOS STATE

**☎** ; 08054178584, 07062539641

## Office stamp

sheet  
content:-

Plan

date :-

AUGUST, 2024

sheet no :-

scale :-

1:100

revision :-

Drawn by :-



Yungola

Checked by :-

Oluwaseun

NOTE:

| SITE ANALYSIS              |                       |
|----------------------------|-----------------------|
| AREA OF THE SITE           | 325.341m <sup>2</sup> |
| AREA OF THE BUILDING       | 120.299m <sup>2</sup> |
| AREA OF THE UNBUILD SPACE  | 199.042m <sup>2</sup> |
| TOTAL LANDSCAPE/GREEN AREA | 31.143m <sup>2</sup>  |
| PERCENTAGE OF BUILD AREA   | 37.5%                 |
| PERCENTAGE OF UNBUILD AREA | 62.5%                 |
| NUMBER OF UNIT             | 1                     |
| TOTAL GROUND FLOOR AREA    | 120.299m <sup>2</sup> |
| TOTAL UPPER FLOOR AREA     | 146.333m <sup>2</sup> |
| NUMBER OF FLOOR            | 2                     |

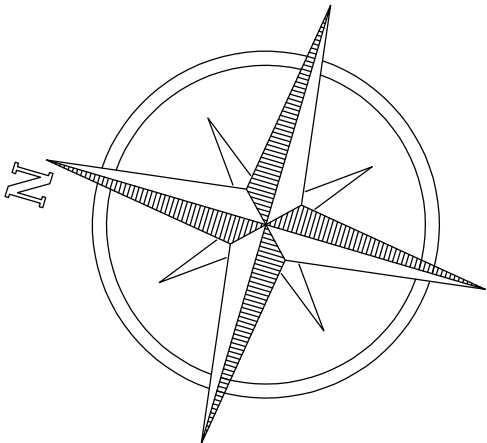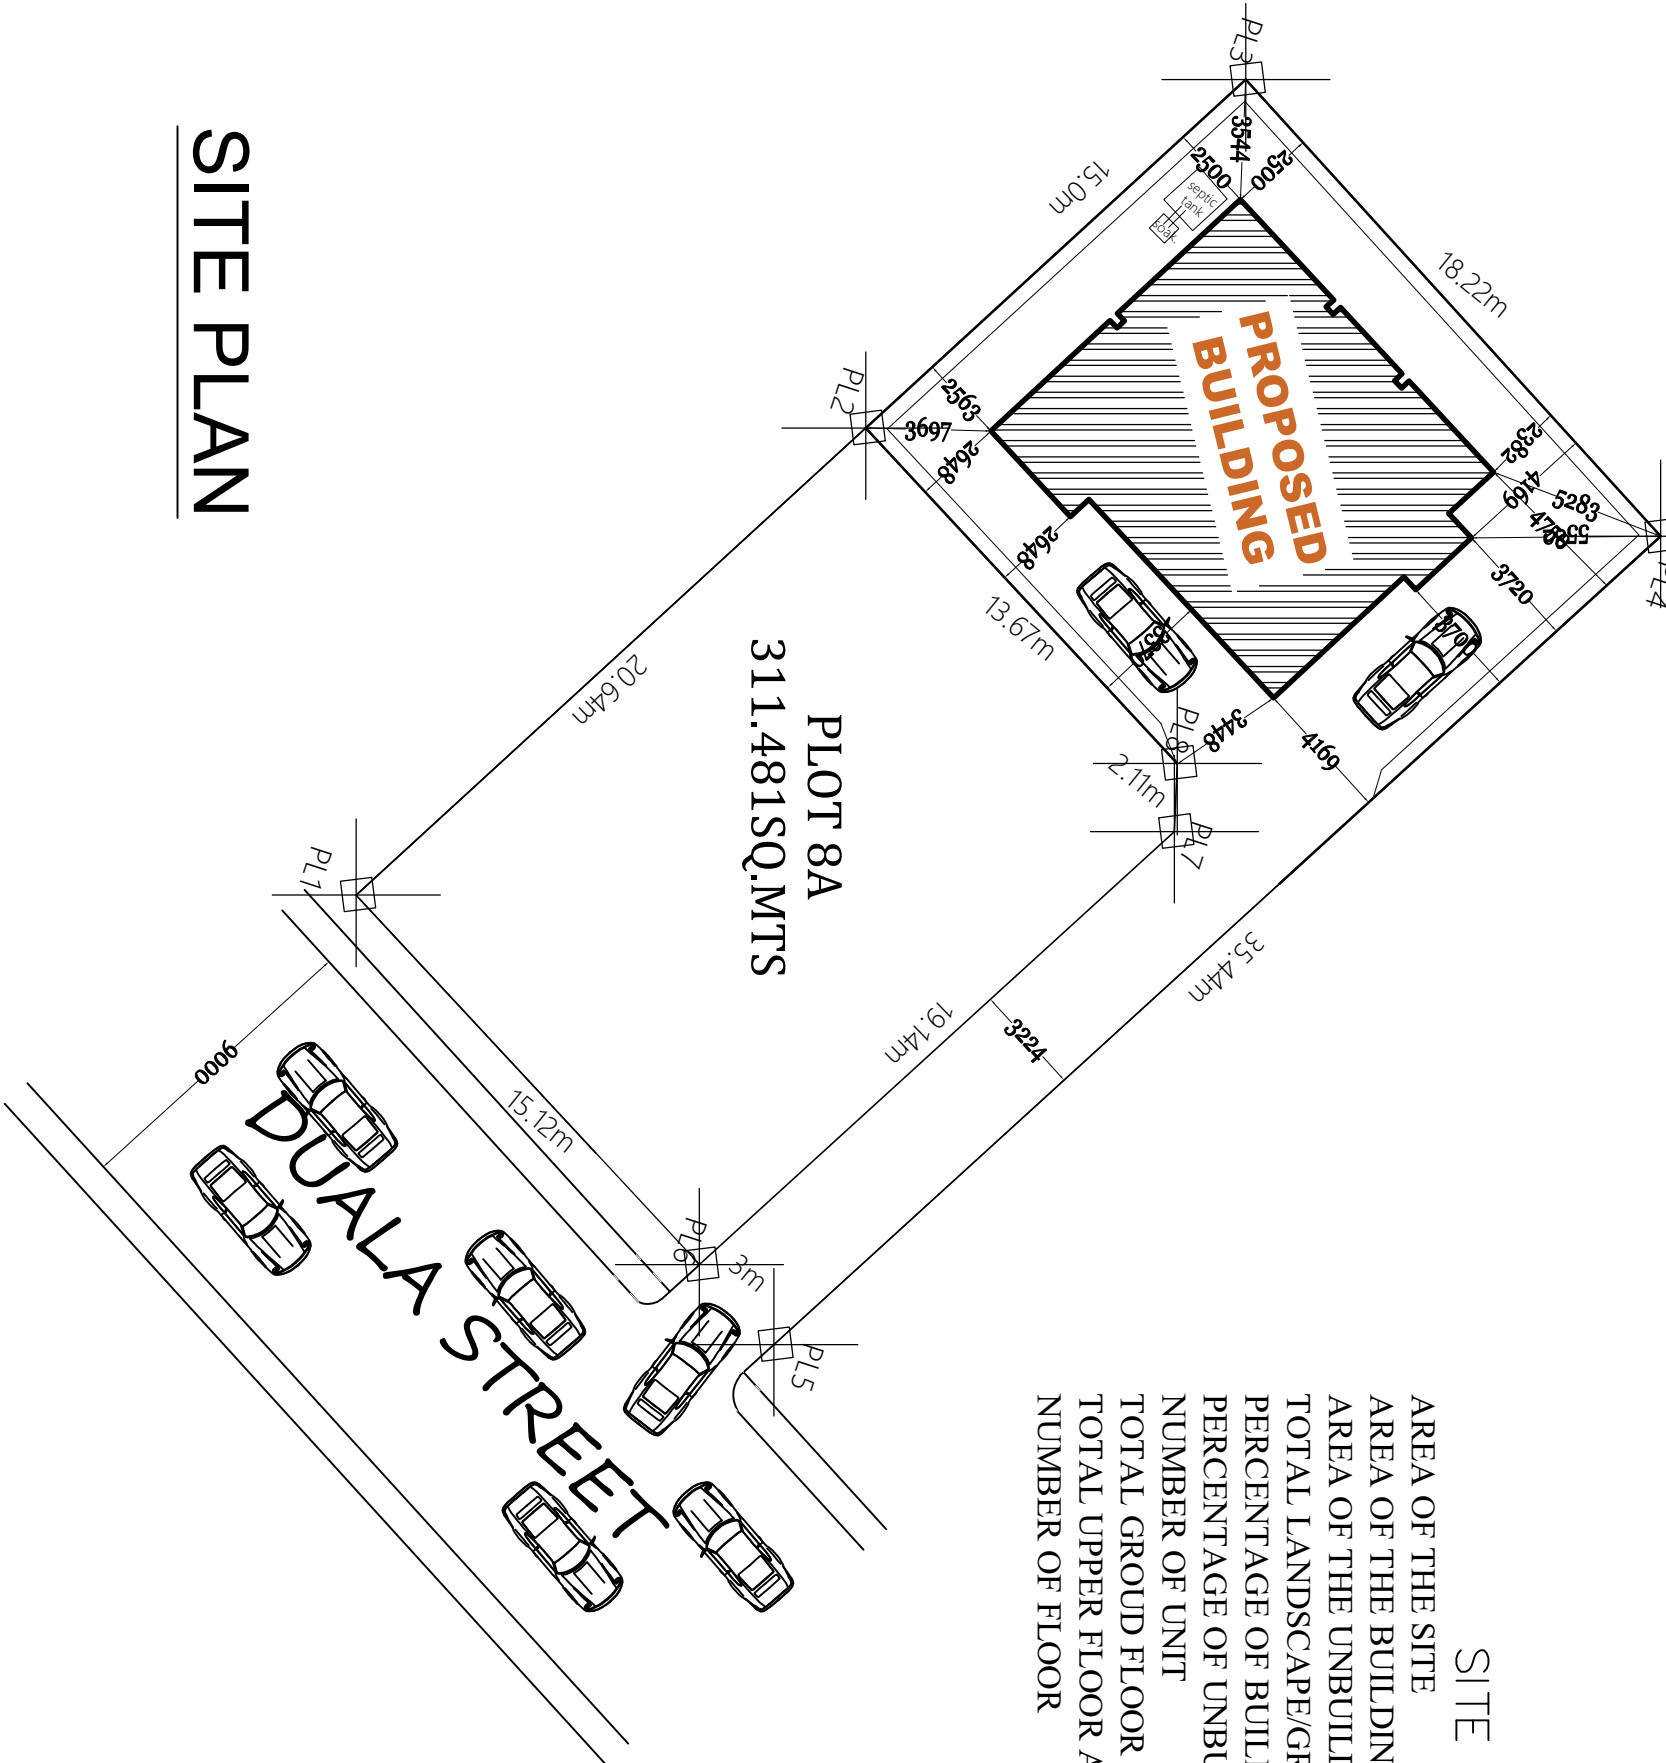

## SITE PLAN

### general note

- 1) The contractor is to check all the drawing before commencing work.
- 2) Any discrepancies observed on this drawing issued by any other party are to be immediately brought to consultant Architect Notice.
- 3) All dimension are in millimeter.
- 4) Dimension are to be confirmed on site.

### Client :-

ADEGBITE USMAN  
OLELEKAN

### Location :-

AT NO. 8B DUALA STREET, CROWN  
ESTATE, SANGOTEDO, ETI-OSA LOCAL  
GOVERNMENT AREA  
LAGOS STATE.

### Project Title :-

Proposed Residential  
Development

Working  
Drawing

### Architech :-

YUNGOLA SERVICES  
LTD. *Re:1783703*

(ARCHITECTURAL DESIGN,  
STRUCTURAL DESIGN,  
BUILDING DEVELOPMENT,  
PLANNER, SUPERVISION

### OFFICE ADDRESS:

NO 2 OSHOGBO STREET, OGUDU,  
LAGOS STATE

**TEL** ; 08054178584, 07062539641

### Office stamp

sheet  
content:-

Plan

date :-

AUGUST, 2024

sheet no :-

scale :-

1:100


revision :-

Drawn by :-

Checked by :-

*Yungola*  
*Oluwaseun*

NOTE:

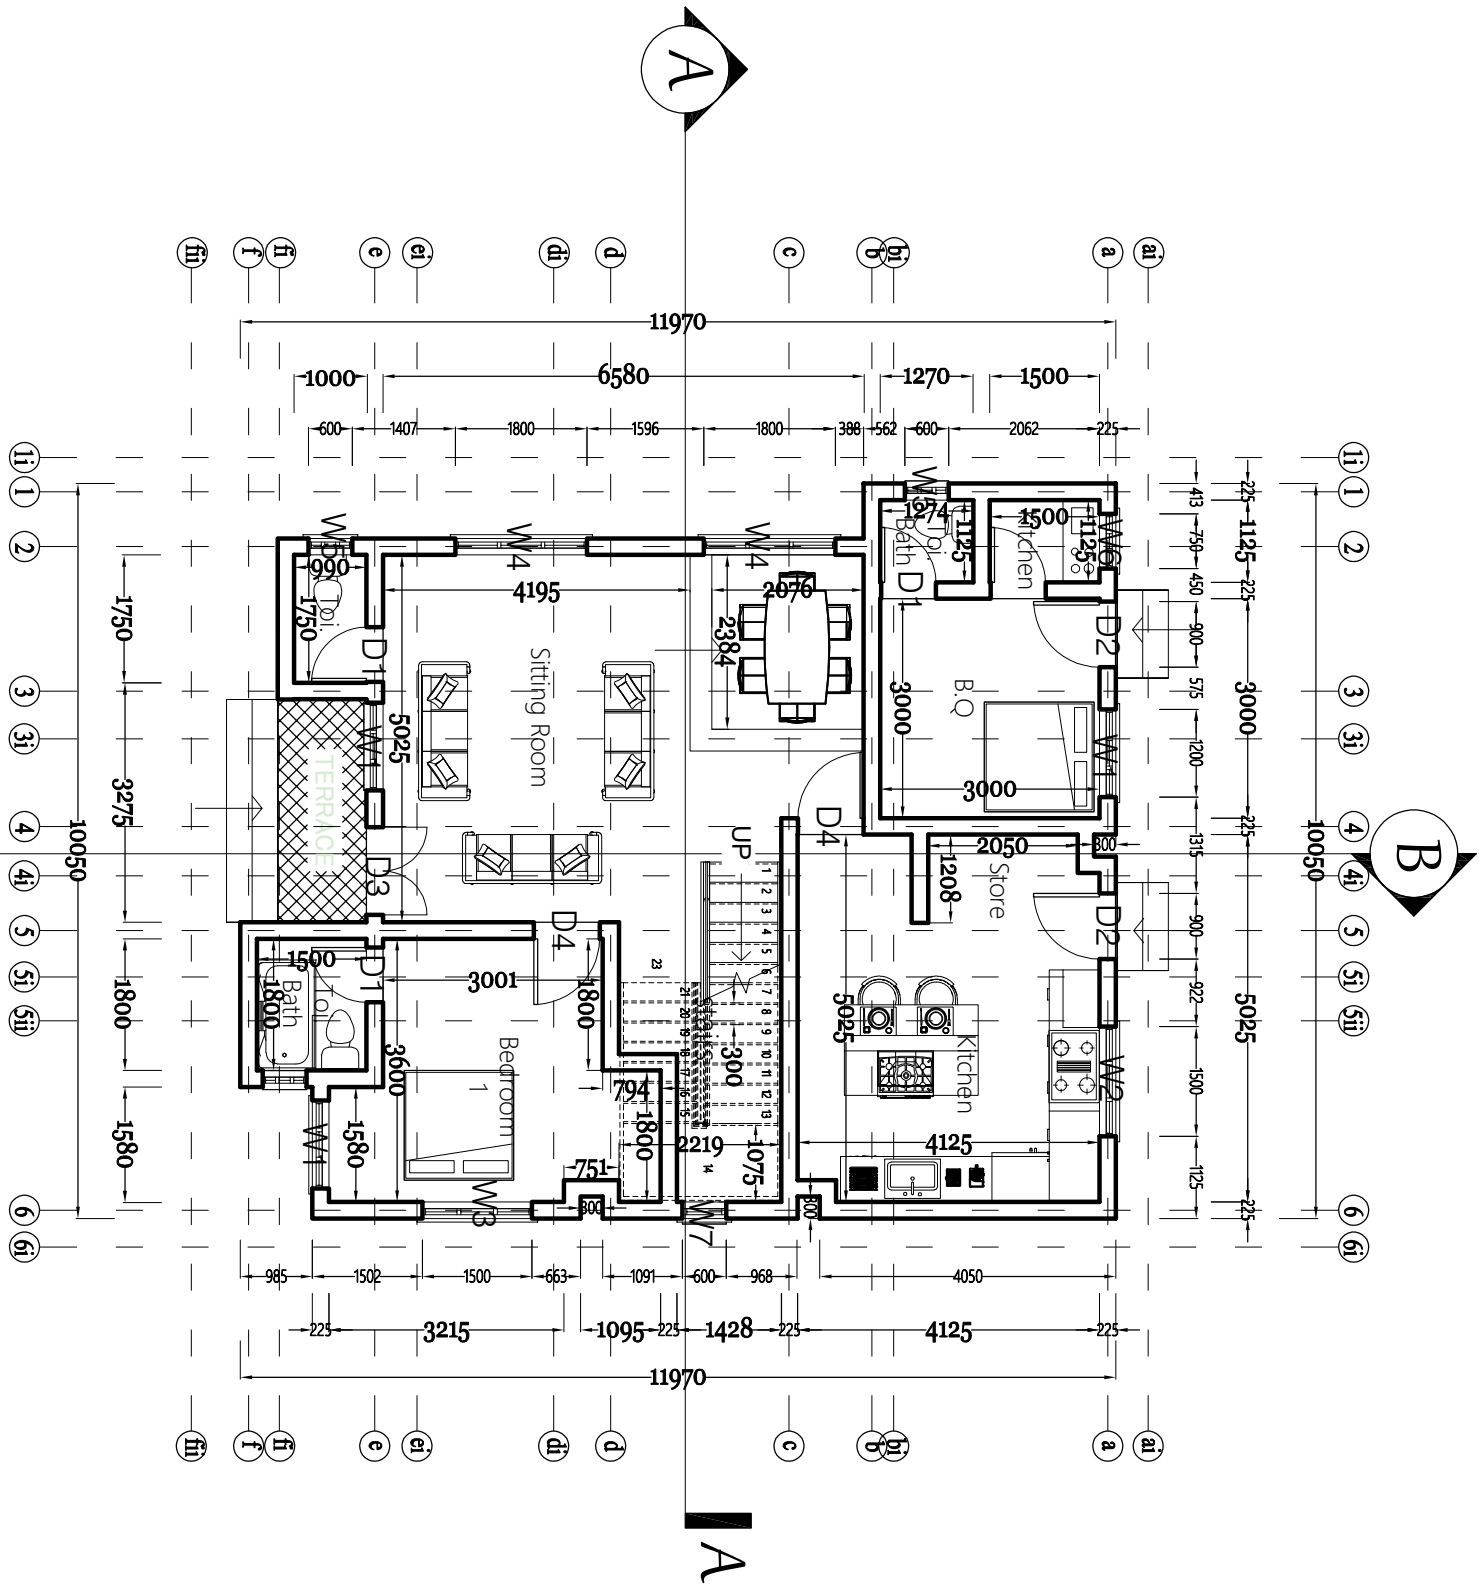

# GROUND FLOOR PLAN

general note

- 1) The contractor is to check all the drawing before commencing work.
- 2) Any discrepancies observed on this drawing issued by any other party are to be immediately brought to consultant Architect Notice.
- 3) All dimension are in millimeter.
- 4) Dimension are to be confirmed on site.

Client :-

ADEGBITE USMAN  
OLALEKAN

Location :-

AT NO. 8B DUALA STREET, CROWN  
ESTATE, SANGOTEDO, ETI-OSA LOCAL  
GOVERNMENT AREA  
LAGOS STATE.

Project Title :-

Proposed Residential  
Development

Working  
Drawing

Architech :-

YUNGOLA SERVICES  
LTD. *Re.1783703*

(ARCHITECTURAL DESIGN,  
STRUCTURAL DESIGN,  
BUILDING DEVELOPMENT,  
PLANNER, SUPERVISION

OFFICE ADDRESS:

NO 2 OSHOGBO STREET, OGUDU,  
LAGOS STATE

**☎** ; 08054178584, 07062539641

Office stamp

sheet  
content:-

Plan

date :-

AUGUST, 2024

sheet no :-

scale :-

1:100

revision :-


Drawn by :-

Yungola

Checked by :-

Oluwaseun

NOTE;

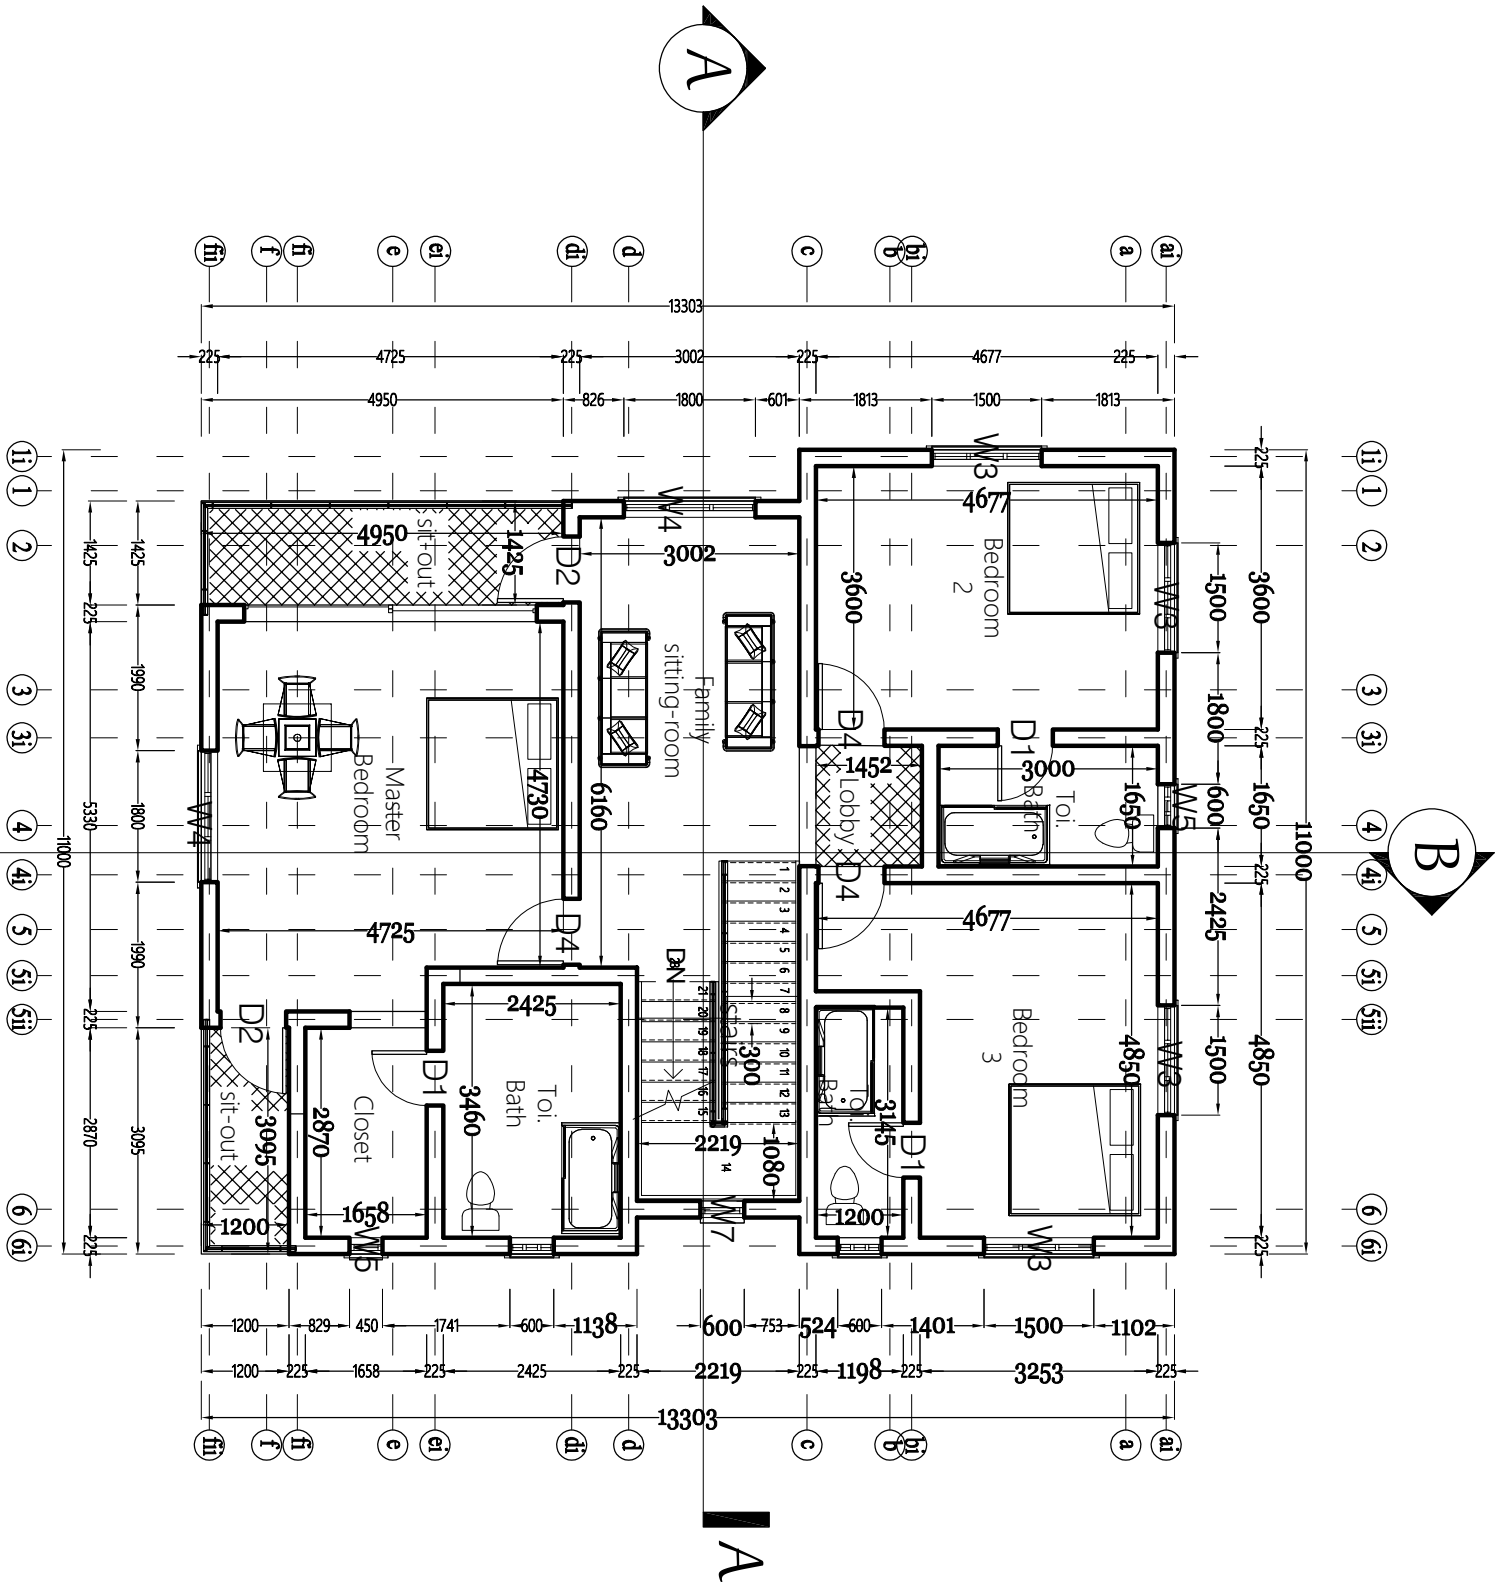

## UPPER FLOOR PLAN

### general note

- 1) The contractor is to check all the drawing before commencing work.
- 2) Any discrepancies observed on this drawing issued by any other party are to be immediately brought to consultant Architect Notice.
- 3) All dimension are in millimeter.
- 4) Dimension are to be confirmed on site.

### Client :-

ADEGBITE USMAN  
OLALEKAN

### Location :-

AT NO. 8B DUALA STREET, CROWN  
ESTATE, SANGOTEDO, ETI-OSA LOCAL  
GOVERNMENT AREA  
LAGOS STATE.

### Project Title :-

Proposed Residential  
Development

Working  
Drawing

### Architech :-

**YUNGOLA SERVICES**  
**LTD.** *Re. 1783703*  
(ARCHITECTURAL DESIGN,  
STRUCTURAL DESIGN,  
BUILDING DEVELOPMENT,  
PLANNER, SUPERVISION  
*OFFICE ADDRESS;*  
NO 2 OSHOGBO STREET, OGUDU,  
LAGOS STATE

**988** ; 08054178584, 070625339641

### Office stamp

sheet  
content:-

Plan

date :-

scale :-

1:100

sheet no :-

revision :-

Drawn by :-

Yungola


Checked by :-

Oluwaseun

AUGUST, 2024

NOTE:

- 0.55mm thick aluminium roofing sheet
- 50mmx75mm hard wood purlin at 900mm c/c
- 50mmx100mm hard wood rafter at 1200mm c/c
- 50mmx100mm hard wood tie beam at 1200mm c/c
- 50mm x 50mm hard wood noggings at 600mm x 600mm c/c
- finished with pop ceilings
- 50mmx100mm hard wood strut
- 25mm x 250mm painted hard wood fascia board

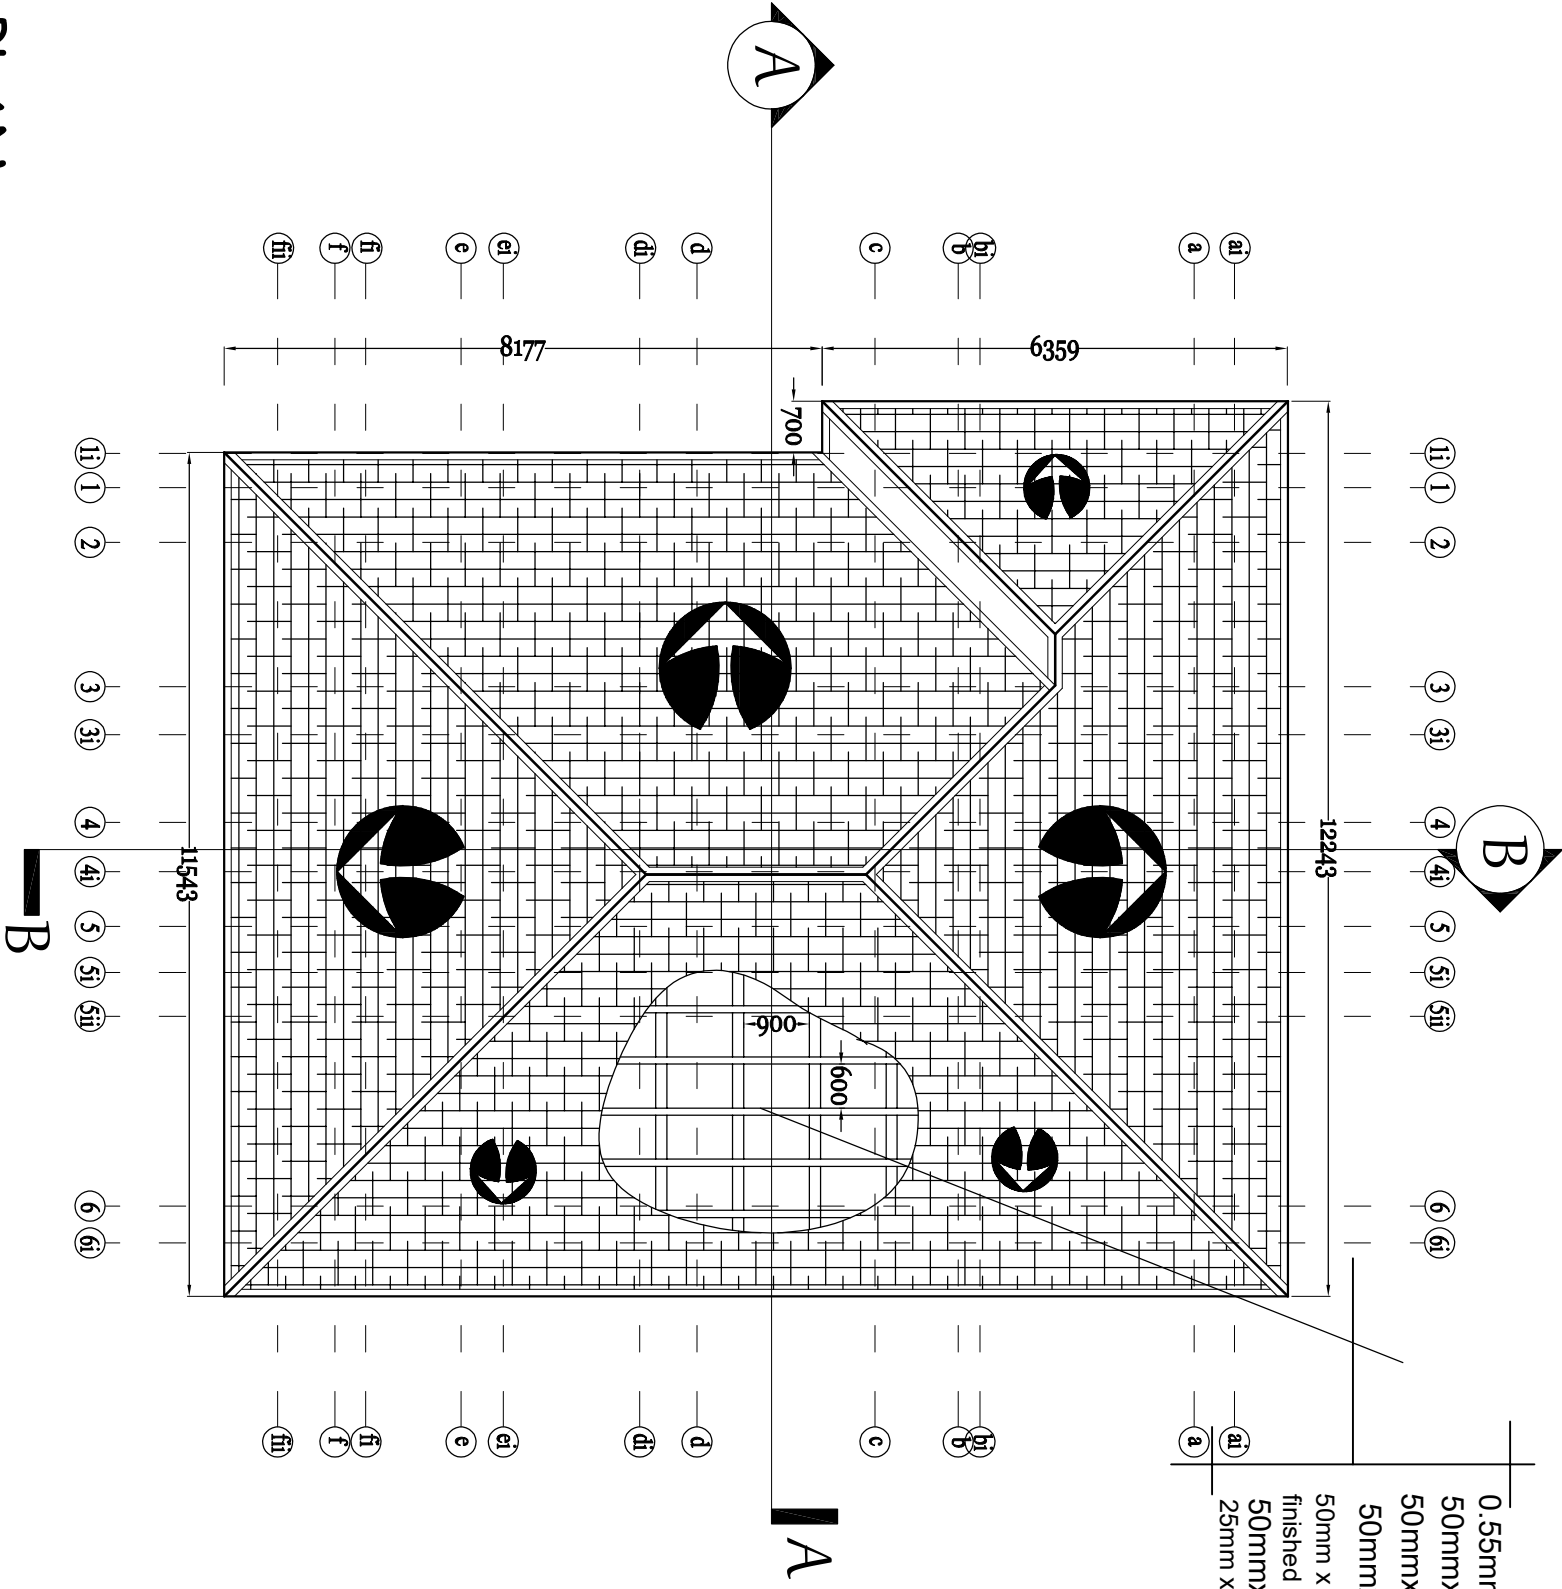

## ROOF PLAN

### general note

- 1) The contractor is to check all the drawing before commencing work.
- 2) Any discrepancies observed on this drawing issued by any other party are to be immediately brought to consultant Architect Notice.
- 3) All dimension are in millimeter.
- 4) Dimension are to be confirmed on site.

### Client :-

ADEGBITE USMAN  
OLELEKAN

### Location :-

AT NO. 8B DUALA STREET, CROWN  
ESTATE, SANGOTEDO, ETI-OSA LOCAL  
GOVERNMENT AREA  
LAGOS STATE.

### Project Title :-

Proposed Residential  
Development

Working  
Drawing

### Architech :-

YUNGOLA SERVICES  
LTD. *Re.1783703*

(ARCHITECTURAL DESIGN,  
STRUCTURAL DESIGN,  
BUILDING DEVELOPMENT,  
PLANNER, SUPERVISION

### OFFICE ADDRESS:

NO 2 OSHOGBO STREET, OGUDU,  
LAGOS STATE

**☎** ; 08054178584, 07062539641

### Office stamp

sheet  
content:-

Plan

date : -

AUGUST, 2024

sheet no :-

scale : -

1:100

revision : -

Drawn by :-


Yungola

Checked by :-

Oluwaseun

NOTE:

- 5.5mm long span aluminium roofing sheet
- 50mmx75mm hard wood purlin at 900mm c/c
- 50mmx100mm hard wood rafter at 1200mm c/c
- 50mmx100mm hard wood tie beam at 1200mm c/c
- 50mm x 50mm hard wood noggings at 600mm x 600mm c/c
- finished with asbestos ceilings
- 50mmx100mm hard wood strut
- 25mm x 250mm painted hard wood fascia board

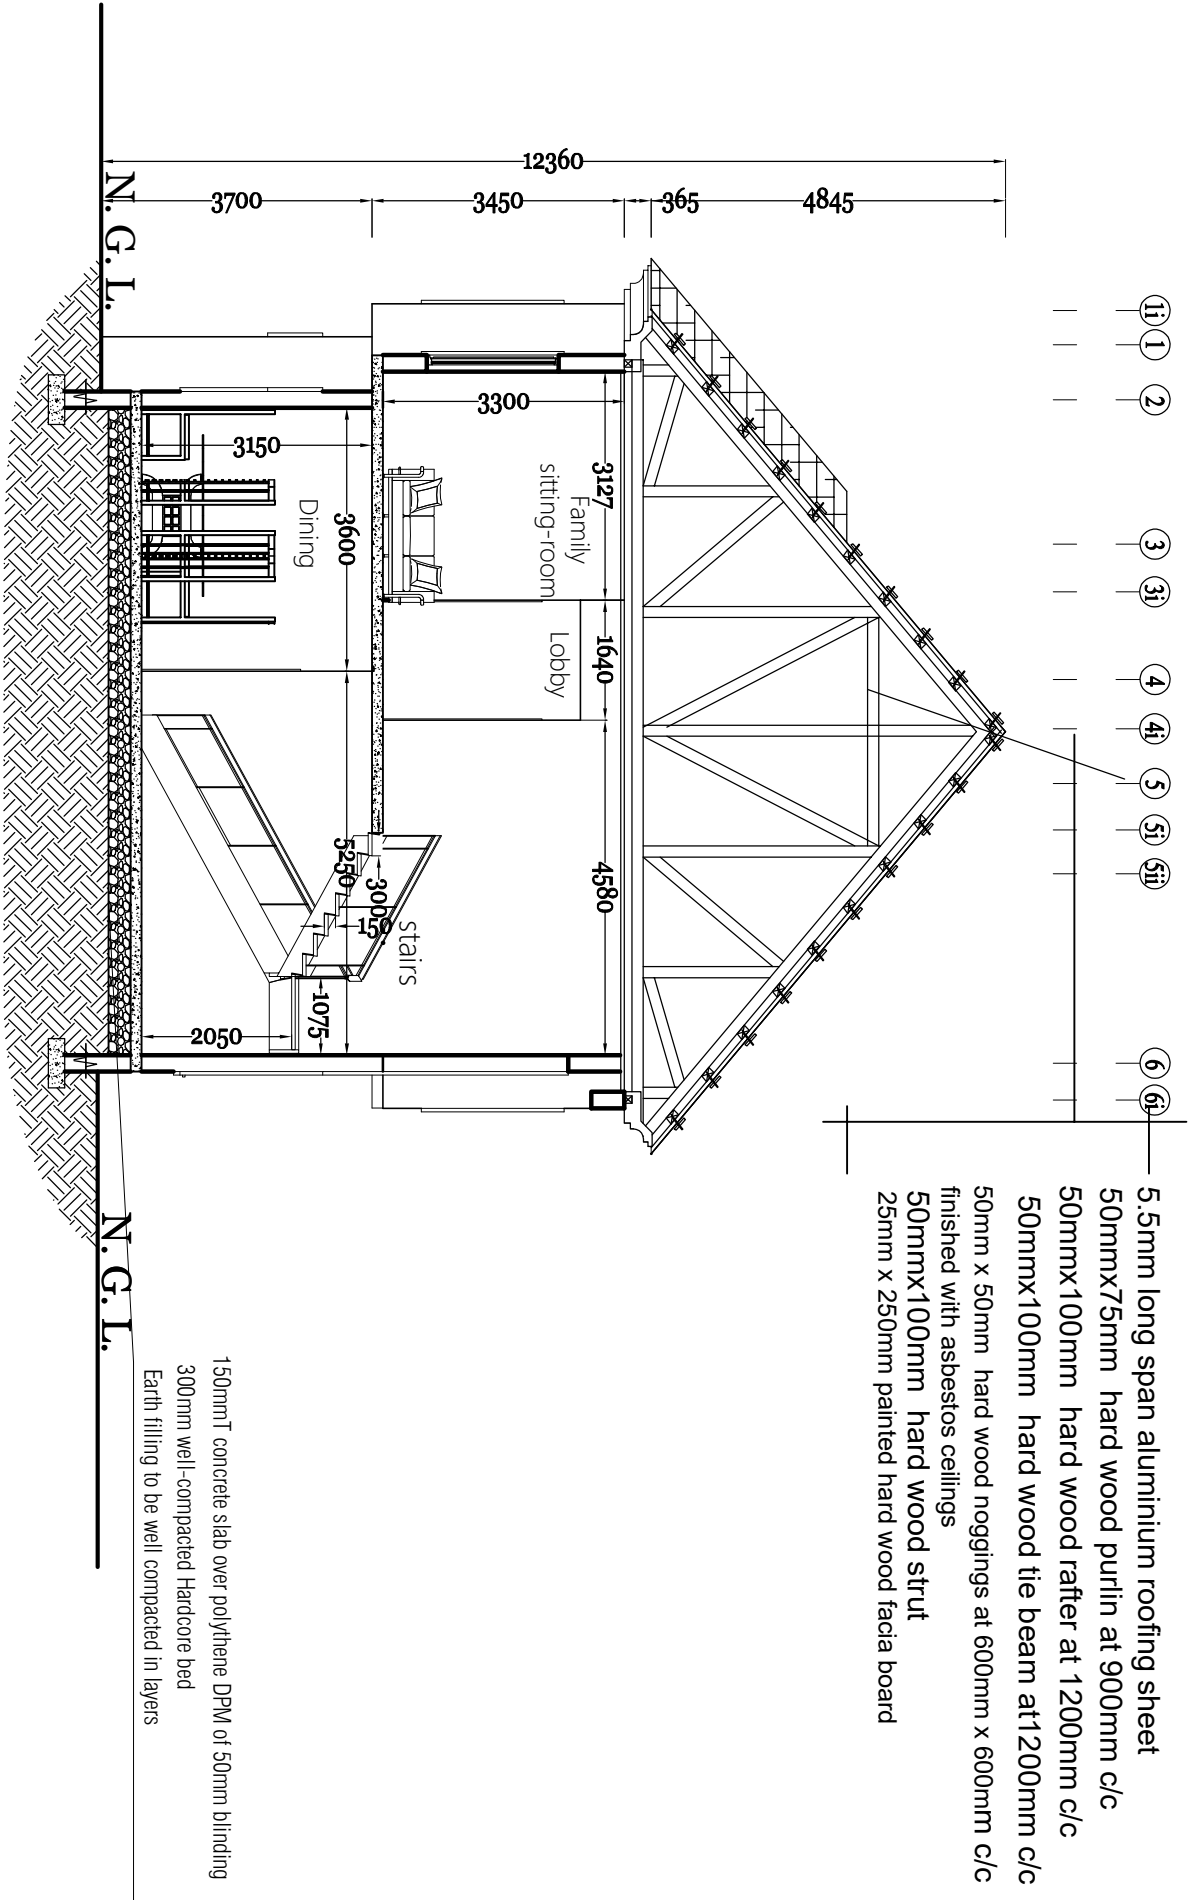

150mmT concrete slab over polythene DPM of 50mm blinding  
300mm well-compacted Hardcore bed  
Earth filling to be well compacted in layers

## SECTION A-A

### general note

- 1) The contractor is to check all the drawing before commencing work.
- 2) Any discrepancies observed on this drawing issued by any other party are to be immediately brought to consultant Architect Notice.
- 3) All dimension are in millimeter.
- 4) Dimension are to be confirmed on site.

### Client :-

ADEGBITE USMAN  
OLALEKAN

### Location :-

AT NO. 8B DUALA STREET, CROWN  
ESTATE, SANGOTEDO, ETI-OSA LOCAL  
GOVERNMENT AREA  
LAGOS STATE.

### Project Title :-

Proposed Residential  
Development

Working  
Drawing

### Architech :-

YUNGOLA SERVICES  
LTD. *Re.1783703*

(ARCHITECTURAL DESIGN,  
STRUCTURAL DESIGN,  
BUILDING DEVELOPMENT,  
PLANNER, SUPERVISION)

### OFFICE ADDRESS:

NO 2 OSHOGBO STREET, OGUDU,  
LAGOS STATE

**TEL** ; 08054178584, 07062539641

### Office stamp

sheet  
content:-

Plan

date :-

AUGUST, 2024

sheet no :-

scale :-

1:100

revision :-

Drawn by :-


Yungola

Checked by :-

Oluwaseun

NOTE:

- 5.5mm long span aluminium roofing sheet
- 50mmx75mm hard wood purlin at 900mm c/c
- 50mmx100mm hard wood rafter at 1200mm c/c
- 50mmx100mm hard wood tie beam at 1200mm c/c
- 50mm x 50mm hard wood noggings at 600mm x 600mm c/c
- finished with asbestos ceilings
- 50mmx100mm hard wood strut
- 25mm x 250mm painted hard wood fascia board

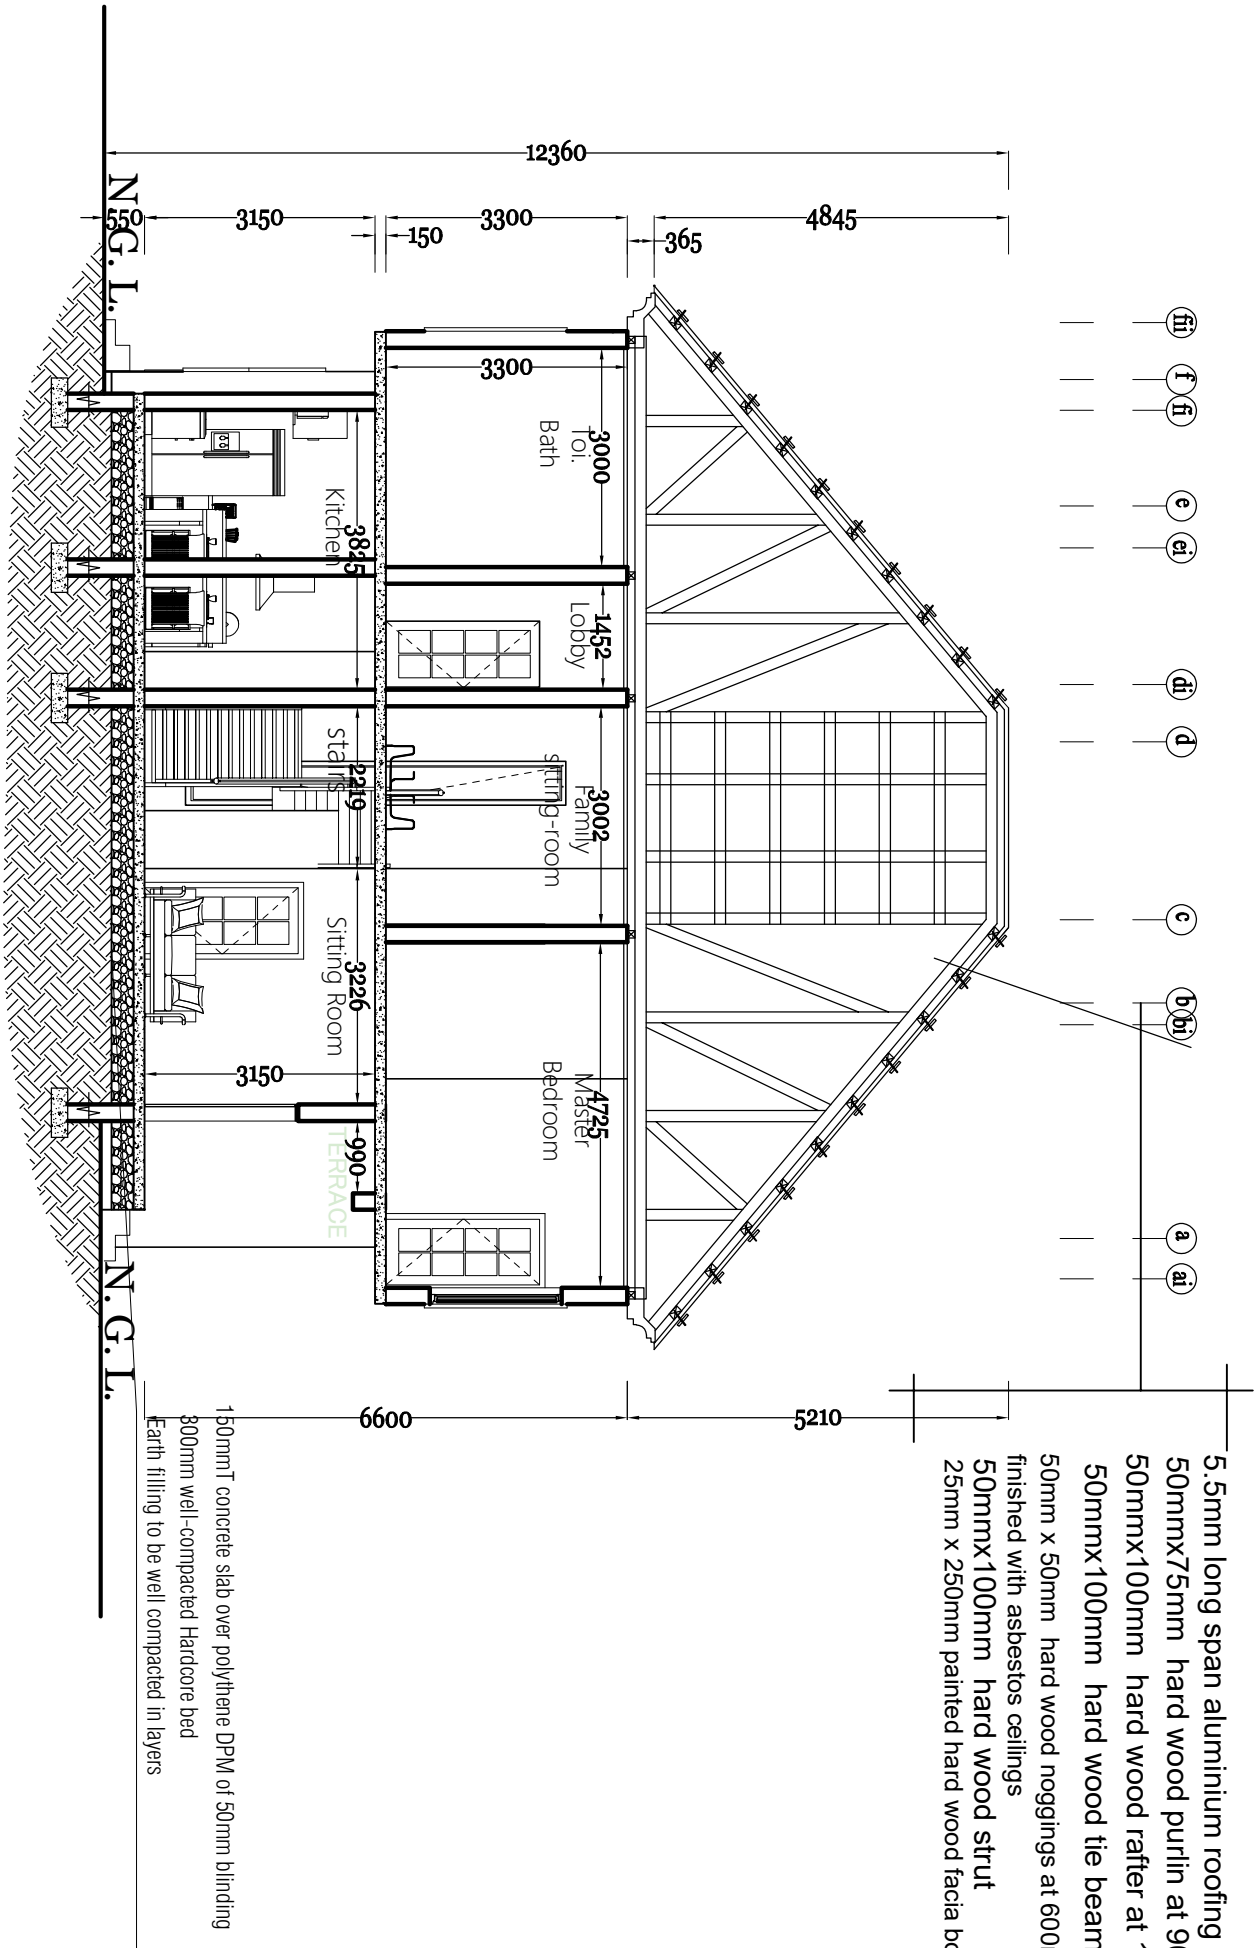

## SECTION B-B

### general note

- 1) The contractor is to check all the drawing before commencing work.
- 2) Any discrepancies observed on this drawing issued by any other party are to be immediately brought to consultant Architect Notice.
- 3) All dimension are in millimeter.
- 4) Dimension are to be confirmed on site.

### Client :-

ADEGBITE USMAN  
OLALEKAN

### Location :-

AT NO. 8B DUALA STREET, CROWN  
ESTATE, SANGOTEDO, ETI-OSA LOCAL  
GOVERNMENT AREA  
LAGOS STATE.

### Project Title :-

Proposed Residential  
Development

Working  
Drawing

### Architech :-

YUNGOLA SERVICES  
LTD. *Re.1783703*

(ARCHITECTURAL DESIGN,  
STRUCTURAL DESIGN,  
BUILDING DEVELOPMENT,  
PLANNER, SUPERVISION

### OFFICE ADDRESS:

NO 2 OSHOGBO STREET, OGUDU,  
LAGOS STATE

**☎** ; 08054178584, 07062539641

### Office stamp

sheet  
content:-

Plan

date :-

AUGUST, 2024

sheet no :-

scale :-

1:100

revision :-



Drawn by :-

Yungola

Checked by :-

Oluwaseun

NOTE:

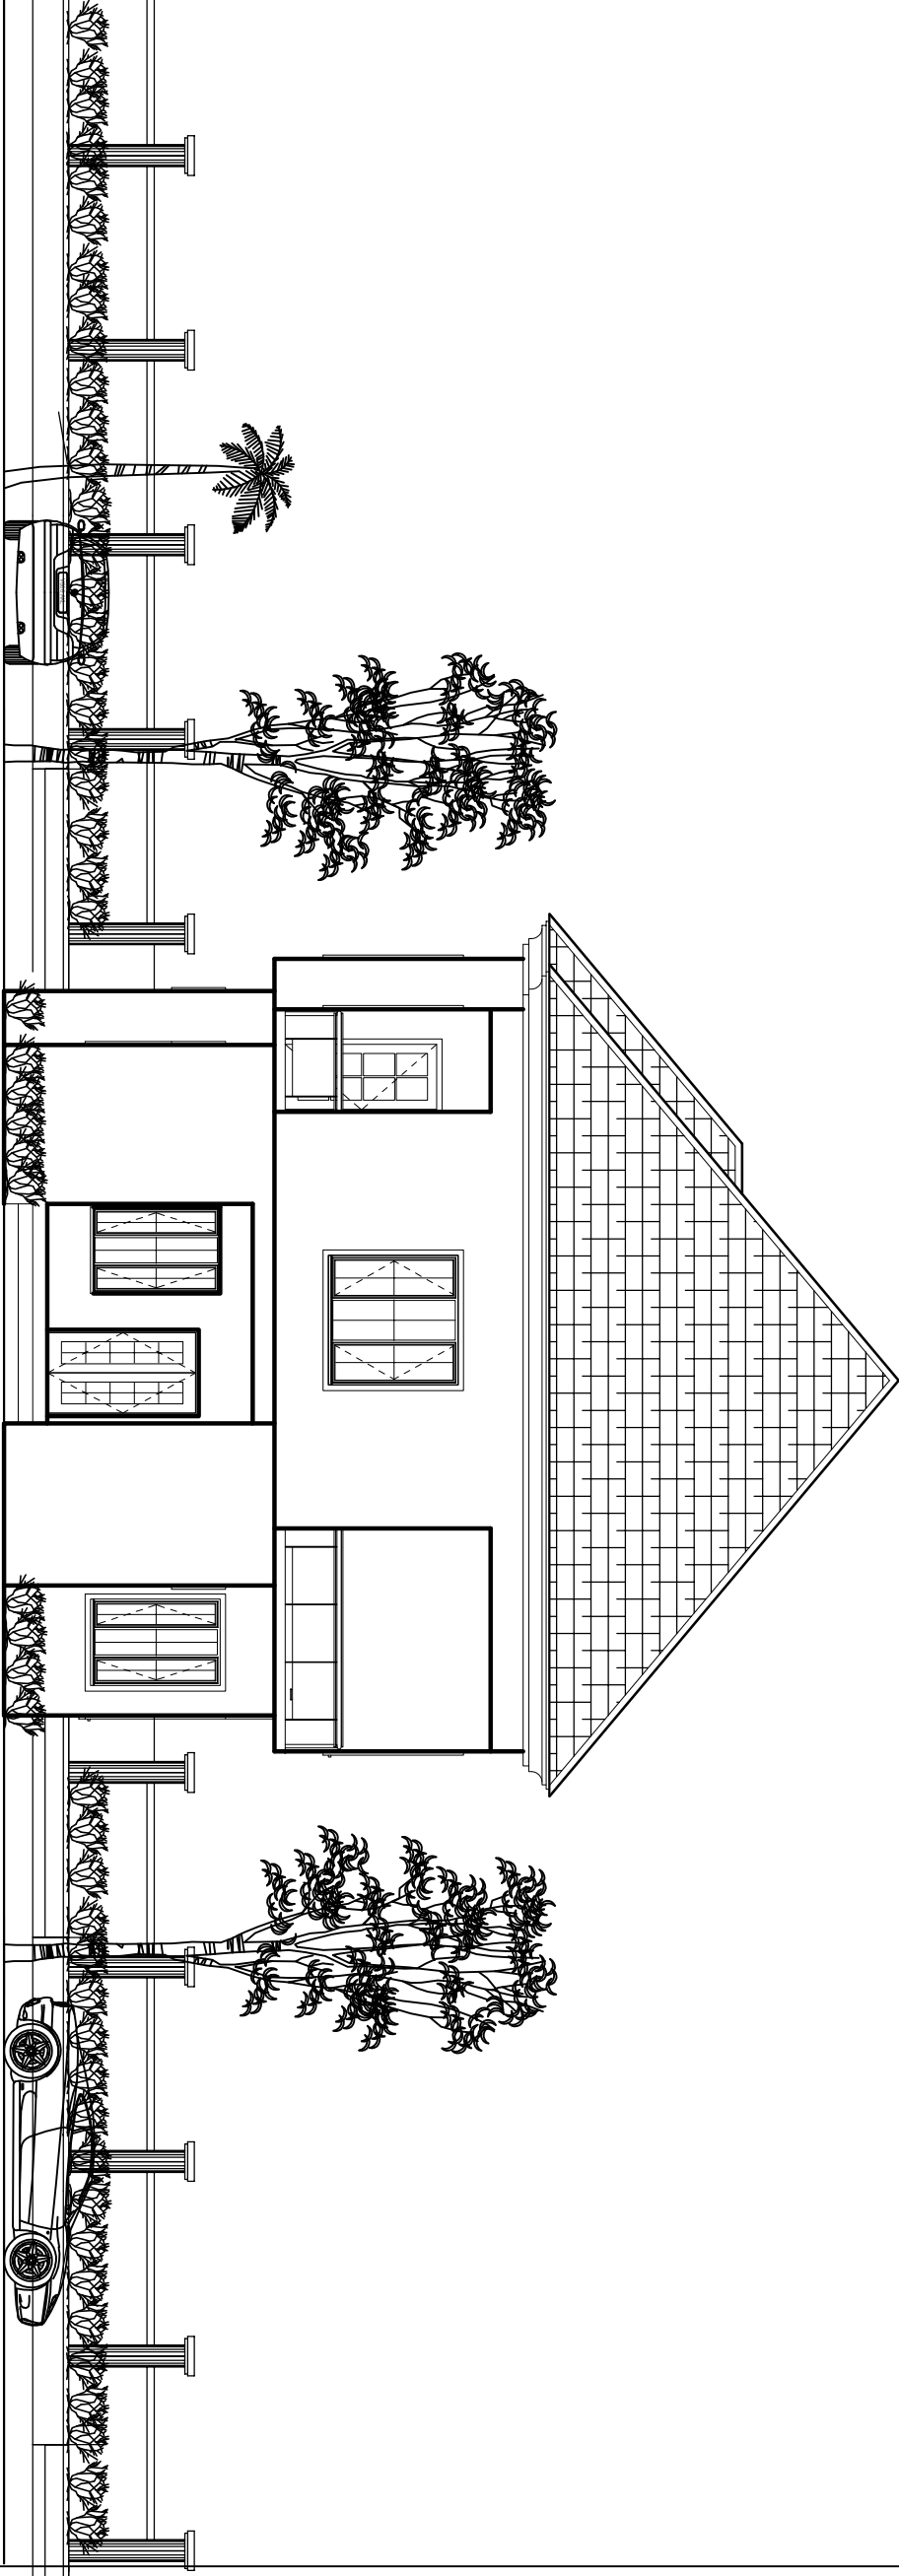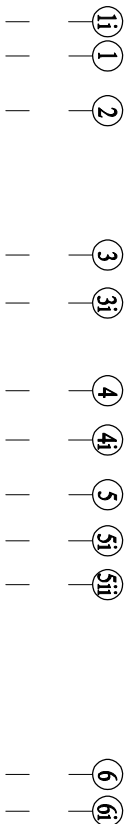

# FRONT VIEW

## general note

- 1) The contractor is to check all the drawing before commencing work.
- 2) Any discrepancies observed on this drawing issued by any other party are to be immediately brought to consultant Architect Notice.
- 3) All dimension are in millimeter.
- 4) Dimension are to be confirmed on site.

## Client :-

ADEGBITE USMAN  
OLALEKAN

## Location :-

AT NO. 8B DUALA STREET, CROWN  
ESTATE, SANGOTEDO, ETI-OSA LOCAL  
GOVERNMENT AREA  
LAGOS STATE.

## Project Title :-

Proposed Residential  
Development

Working  
Drawing

## Architech :-

YUNGOLA SERVICES  
LTD. *Re.1783703*

(ARCHITECTURAL DESIGN,  
STRUCTURAL DESIGN,  
BUILDING DEVELOPMENT,  
PLANNER, SUPERVISION

## OFFICE ADDRESS:

NO 2 OSHOGBO STREET, OGUDU,  
LAGOS STATE

**☎** ; 08054178584, 07062539641

## Office stamp

sheet  
content:-

Plan

date : -

AUGUST, 2024

sheet no :-

scale : -

1:100

revision : -


Drawn by :-

*Yungola*

Checked by :-

*Oluwaseun*

NOTE:

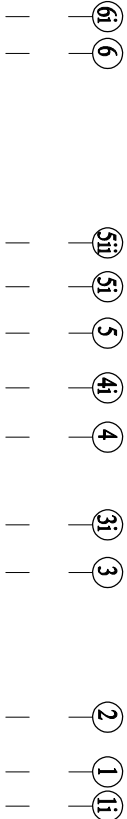

## BACK VIEW

### general note

- 1) The contractor is to check all the drawing before commencing work.
- 2) Any discrepancies observed on this drawing issued by any other party are to be immediately brought to consultant Architect Notice.
- 3) All dimension are in millimeter.
- 4) Dimension are to be confirmed on site.

### Client :-

ADEGBITE USMAN  
OLALEKAN

### Location :-

AT NO. 8B DUALA STREET, CROWN  
ESTATE, SANGOTEDO, ETI-OSA LOCAL  
GOVERNMENT AREA  
LAGOS STATE.

### Project Title :-

Proposed Residential  
Development

Working  
Drawing

### Architech :-

YUNGOLA SERVICES  
LTD. *Re.1783703*

(ARCHITECTURAL DESIGN,  
STRUCTURAL DESIGN,  
BUILDING DEVELOPMENT,  
PLANNER, SUPERVISION

### OFFICE ADDRESS:

NO 2 OSHOGBO STREET, OGUDU,  
LAGOS STATE

**☎** ; 08054178584, 07062539641

### Office stamp

sheet  
content:-

Plan

date : -

AUGUST, 2024

sheet no :-

scale : -

1:100

revision : -



Drawn by :-

*Yungola*

Checked by :-

*Oluwaseun*

NOTE:

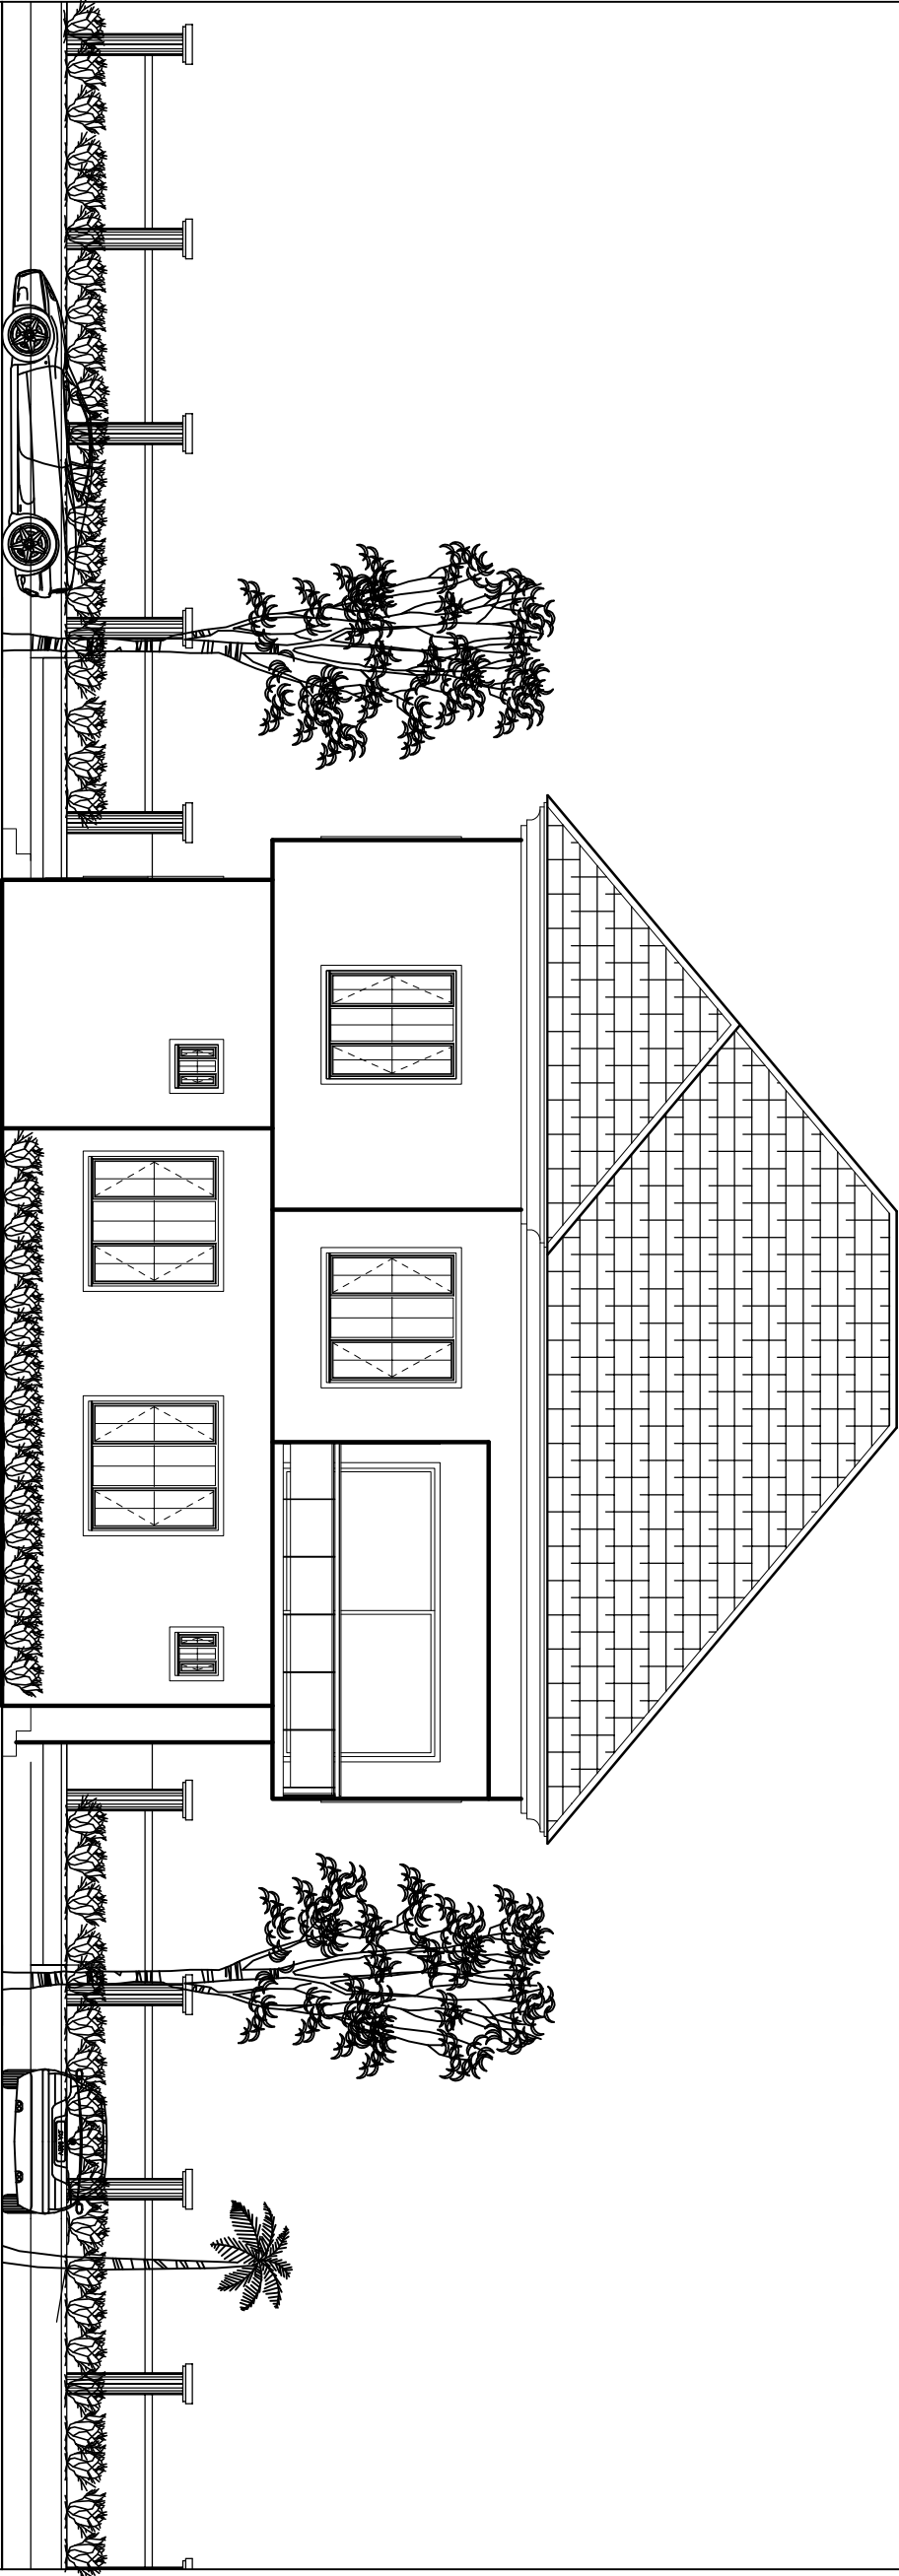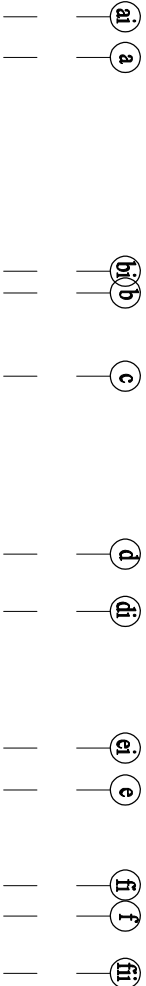

# RIGHT VIEW

## general note

- 1) The contractor is to check all the drawing before commencing work.
- 2) Any discrepancies observed on this drawing issued by any other party are to be immediately brought to consultant Architect Notice.
- 3) All dimension are in millimeter.
- 4) Dimension are to be confirmed on site.

## Client :-

ADEGBITE USMAN  
OLALEKAN

## Location :-

AT NO. 8B DUALA STREET, CROWN  
ESTATE, SANGOTEDO, ETI-OSA LOCAL  
GOVERNMENT AREA  
LAGOS STATE.

## Project Title :-

Proposed Residential  
Development

Working  
Drawing

## Architech :-

YUNGOLA SERVICES  
LTD. *Re.1783703*

(ARCHITECTURAL DESIGN,  
STRUCTURAL DESIGN,  
BUILDING DEVELOPMENT,  
PLANNER, SUPERVISION)

## OFFICE ADDRESS:

NO 2 OSHOGBO STREET, OGUDU,  
LAGOS STATE

**TEL** ; 08054178584, 07062539641

## Office stamp

sheet  
content:-

Plan

sheet no :-

scale :-

1:100

date :-

AUGUST, 2024

revision :-



Drawn by :-

Yungola

Checked by :-

Oluwaseun

NOTE:

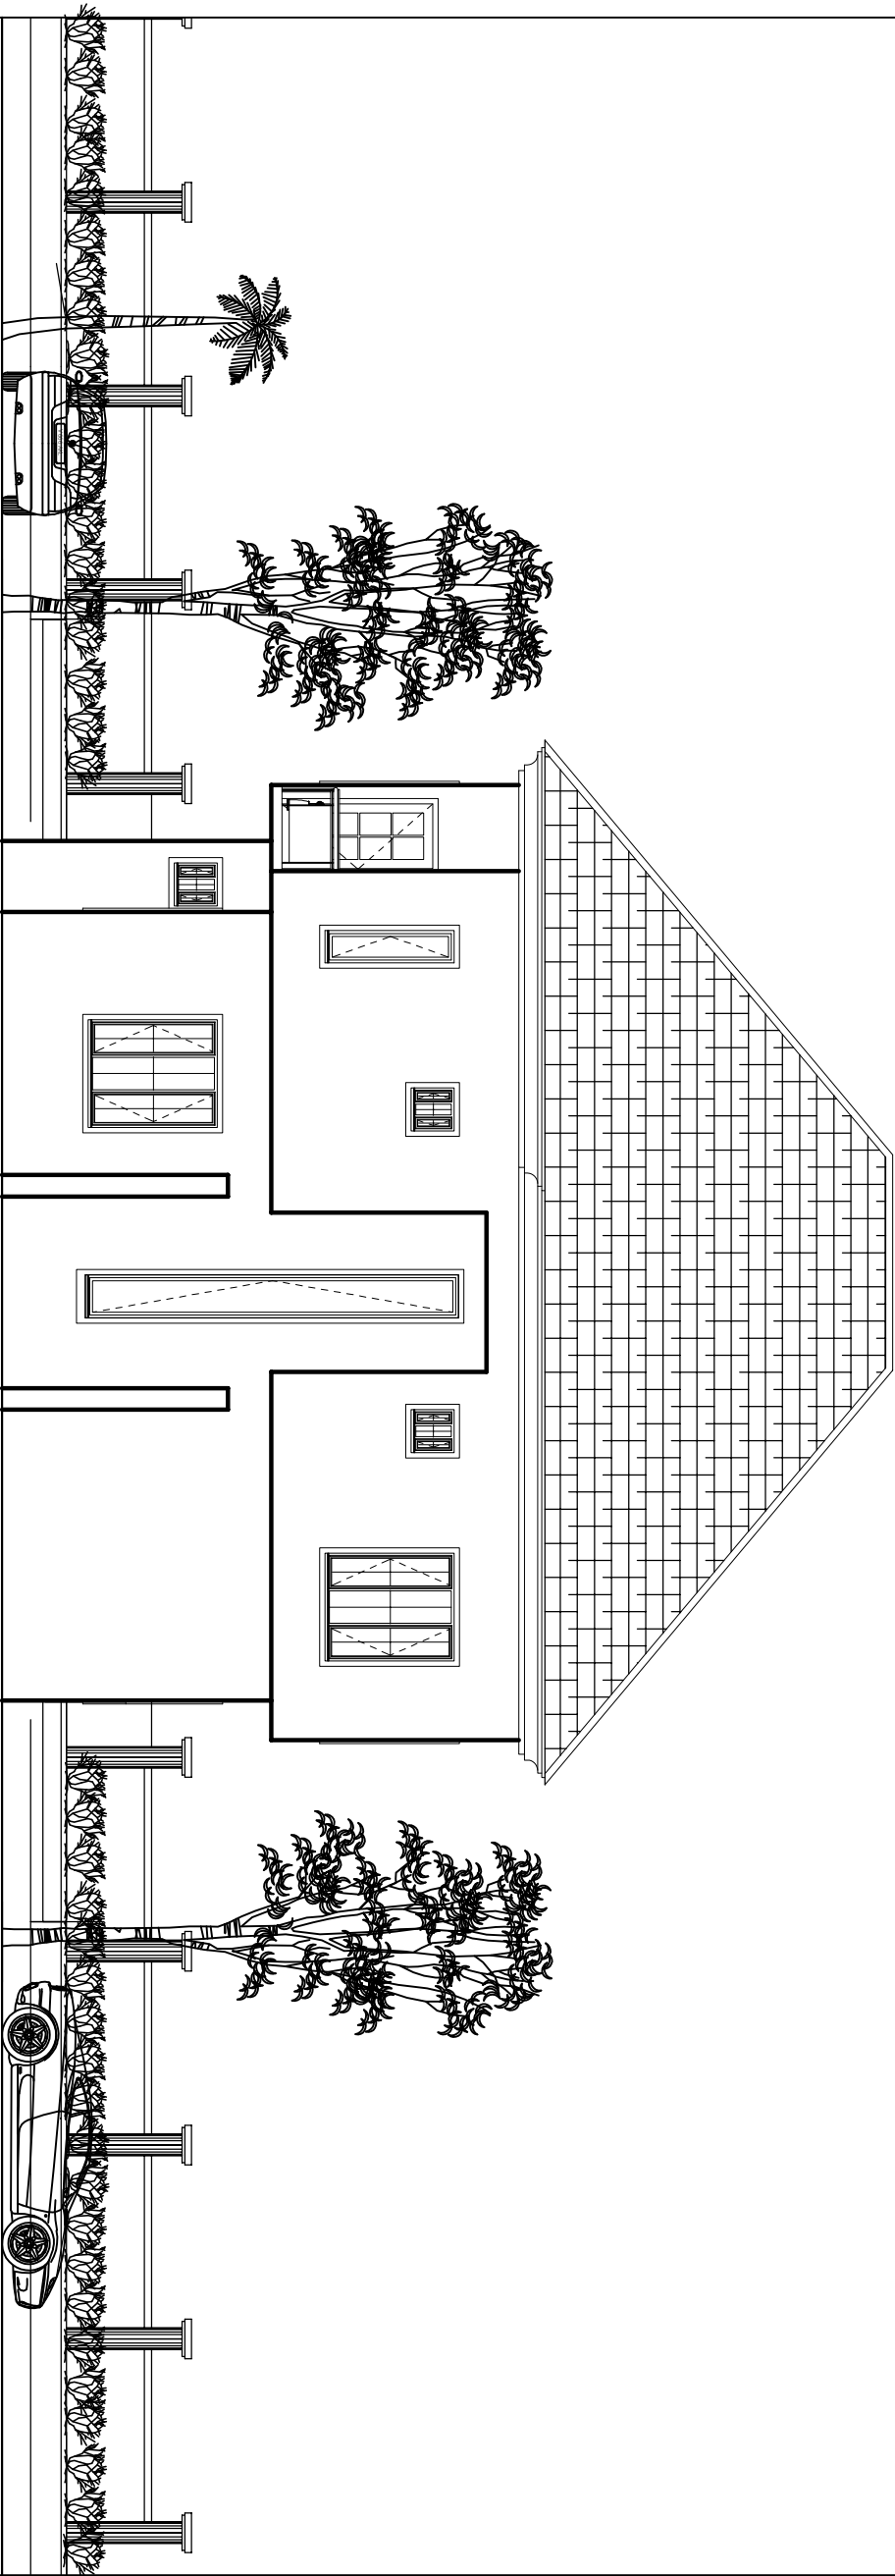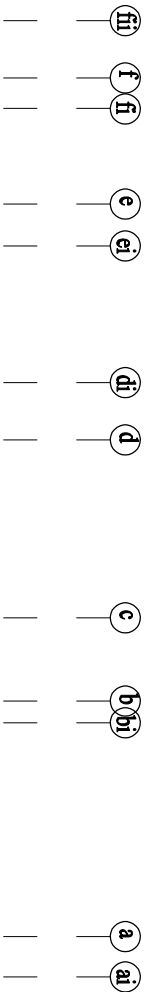

## LEFT VIEW

### general note

- 1) The contractor is to check all the drawing before commencing work.
- 2) Any discrepancies observed on this drawing issued by any other party are to be immediately brought to consultant Architect Notice.
- 3) All dimension are in millimeter.
- 4) Dimension are to be confirmed on site.

### Client :-

ADEGBITE USMAN  
OLALEKAN

### Location :-

AT NO. 8B DUALA STREET, CROWN  
ESTATE, SANGOTEDO, ETI-OSA LOCAL  
GOVERNMENT AREA  
LAGOS STATE.

### Project Title :-

Proposed Residential  
Development

Working  
Drawing

### Architech :-

YUNGOLA SERVICES  
LTD. *Re.1783703*

(ARCHITECTURAL DESIGN,  
STRUCTURAL DESIGN,  
BUILDING DEVELOPMENT,  
PLANNER, SUPERVISION

### OFFICE ADDRESS:

NO 2 OSHOGBO STREET, OGUDU,  
LAGOS STATE

**☎** ; 08054178584, 07062539641

### Office stamp

sheet  
content:-

Plan

date : -

sheet no :-

scale : -

1:100

revision : -

Drawn by :-

Yungola








Checked by :-

Oluwaseun





AUGUST, 2024

NOTE:

WINDOWS SCHEDULE
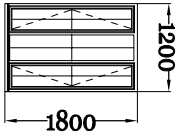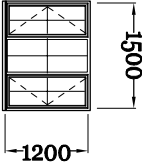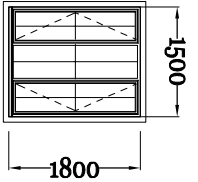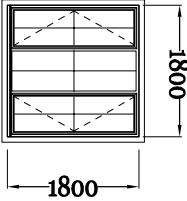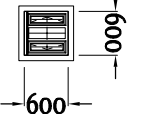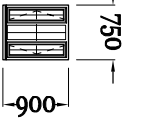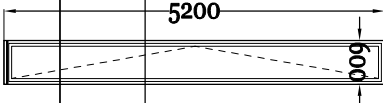
|                |                                                                                     |                                                                                     |                                                                                       |                                                                                       |                                                                                       |                                                                                       |                                                                                       |
|----------------|-------------------------------------------------------------------------------------|-------------------------------------------------------------------------------------|---------------------------------------------------------------------------------------|---------------------------------------------------------------------------------------|---------------------------------------------------------------------------------------|---------------------------------------------------------------------------------------|---------------------------------------------------------------------------------------|
| PROFILE        |  |  |  |  |  |  |  |
| LABEL ON PLAN  | W1                                                                                  | W2                                                                                  | W3                                                                                    | W4                                                                                    | W5                                                                                    | W6                                                                                    | W7                                                                                    |
| NO'S REQD      | 3                                                                                   | 1                                                                                   | 5                                                                                     | 4                                                                                     | 4                                                                                     | 1                                                                                     | 1                                                                                     |
| DESCRIPTION    | Aluminum casement windows with burglary bars, fly and mosquito screen               |                                                                                     |                                                                                       |                                                                                       |                                                                                       |                                                                                       |                                                                                       |
| DIMENSION (MM) | 1200 X 1500                                                                         | 1500 X 1200                                                                         | 1500 X 1800                                                                           | 1800 X 1800                                                                           | 600 X 600                                                                             | 750 X 900                                                                             | 600 X 5200                                                                            |

DOORS SCHEDULE
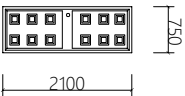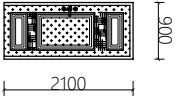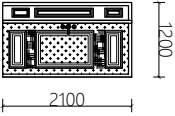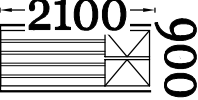
|                |   |   |   |   |
|----------------|---|---|---|---|
| PROFILE        |                          |                          |                          |                          |
| LABEL ON PLAN  | D1   | D2   | D3   | D4   |
| NO'S REQD      | 6   | 4   | 1   | 5   |
| DESCRIPTION    | Single action, single leaf steel panel door with steel frame see manufacturers fixing catalogue for details. | Single action, single leaf steel panel door with steel frame see manufacturers fixing catalogue for details. | Double action, Double leaf steel panel door with steel frame see manufacturers fixing catalogue for details. | Single action, single leaf steel panel door with steel frame see manufacturers fixing catalogue for details. |
| DIMENSION (MM) | 750 X 2100                                                                                                   | 900 X 2100                                                                                                   | 1200 X 2100                                                                                                  | 900 X 2100                                                                                                   |

SCHEDULE

**general note**

1) The contractor is to check all the drawing before commencing work.  
2) Any discrepancies observed on this drawing issued by any other party are to be immediately brought to consultant Architect Notice.  
3) All dimension are in millimeter.  
4) Dimension are to be confirmed on site.

**Client :-**  
**ADEGBITE USMAN**  
**OLALEKAN**

**Location :-**  
AT NO. 8B DUALA STREET, CROWN ESTATE, SANGOTEDO, ETI-OSA LOCAL GOVERNMENT AREA LAGOS STATE.

**Project Title :-**  
**Proposed Residential Development**

**Architech :-**  
**YUNGOLA SERVICES LTD.** *Re.1783703*  
(ARCHITECTURAL DESIGN, STRUCTURAL DESIGN, BUILDING DEVELOPMENT, PLANNER, SUPERVISION)  
**OFFICE ADDRESS:**  
NO 2 OSHOGBO STREET, OGUDU, LAGOS STATE  
**☎** ; 08054178584, 07062539641

**Office stamp**

sheet content:-

Plan

date : -

sheet no :-

scale : -

1:100

revision : -





Drawn by :- *Yungola*

Checked by :- *Oluwaseun*


NOTE:

## DETAILS

TYPICAL SOAKWAY AND SEPTIC TANK DETAILS

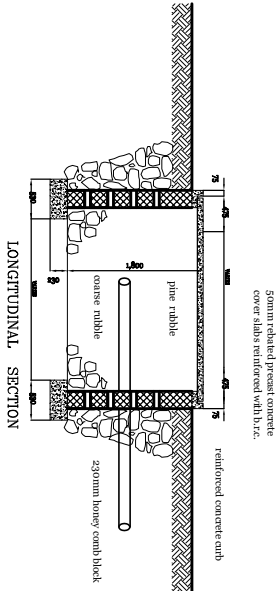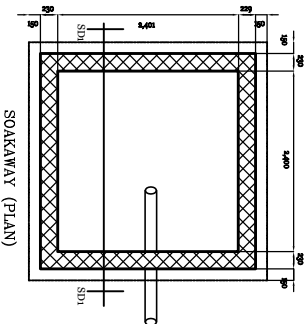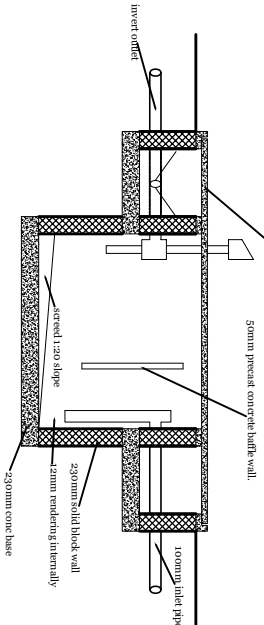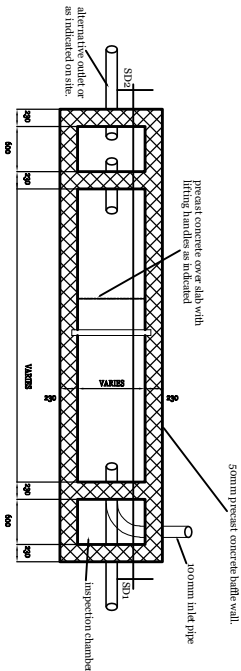


## FENCE





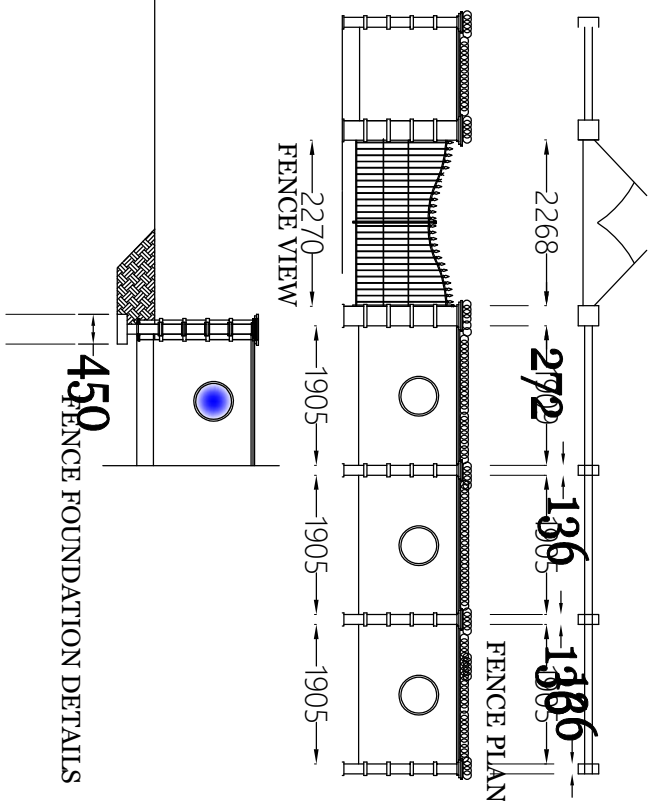


| 1         | 2            | 3                | 4                | 5      | 6       | 7     | 8      | 9        | 10      |
|-----------|--------------|------------------|------------------|--------|---------|-------|--------|----------|---------|
| TANK TYPE | NO. of users | CAPACITY OF TANK | PER UNIT OF TANK | LENGTH | BREADTH | DEPTH | OUTLET | USE TYPE | AVERAGE |
| A         | 10           | 0.187            | 1.1820           | 2400   | 600     | 1275  | 1200   | 900      | 1800    |
| B         | 15           | 0.098            | 1.470            | 2775   | 825     | 1275  | 1200   | 1125     | 1800    |
| C         | 20           | 0.084            | 1.680            | 3000   | 1050    | 1350  | 1275   | 1200     | 1800    |
| D         | 50           | 0.070            | 3.500            | 3600   | 1200    | 1575  | 1500   | 1500     | 1800    |
| E         | 100          | 0.070            | 7.000            | 4800   | 1950    | 1650  | 1575   | 2100     | 1800    |
| F         | 200          | 0.070            | 14.000           | 6000   | 2450    | 1875  | 1800   | 2700     | 1800    |

TYPICAL SECTION THROUGH LINTEL

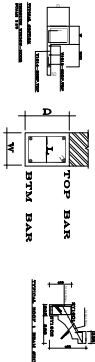

| LINTEL SCHEDULE |       |       |                 |       |            |  |  |  |  |
|-----------------|-------|-------|-----------------|-------|------------|--|--|--|--|
| CLEAR SPAN      | DEPTH | WIDTH | PTH BAR/TPS BAR | LINKS |            |  |  |  |  |
| 000-1500        | 225   | 225   | S-Y18           | S-Y18 | Y10-250c/c |  |  |  |  |
| 1500-1800       | 225   | 225   | S-Y18           | S-Y18 | Y10-250c/c |  |  |  |  |
| 1800-2400       | 300   | 225   | S-Y18           | S-Y18 | Y10-250c/c |  |  |  |  |
| 2400-3000       | 300   | 225   | S-Y18           | S-Y18 | Y10-250c/c |  |  |  |  |

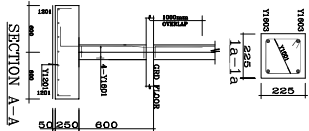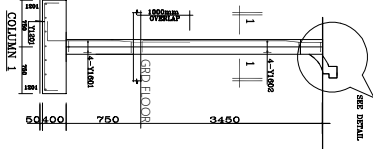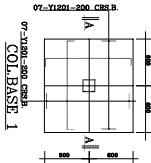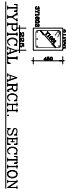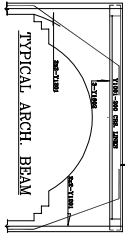

### general note

- 1) The contractor is to check all the drawing before commencing work.
- 2) Any discrepancies observed on this drawing issued by any other party are to be immediately brought to consultant Architect Notice.
- 3) All dimension are in millimeter.
- 4) Dimension are to be confirmed on site.

### Client :-

ADEGBITE USMAN  
OLALEKAN

### Location :-

AT NO. 8B DUALA STREET, CROWN  
ESTATE, SANGOTEDO, ETI-OSA LOCAL  
GOVERNMENT AREA  
LAGOS STATE.

### Project Title :-

Proposed Residential  
Development

Working  
Drawing

### Architech :-

YUNGOLA SERVICES  
LTD. *Re.1783703*  
(ARCHITECTURAL DESIGN,  
STRUCTURAL DESIGN,  
BUILDING DEVELOPMENT,  
PLANNER, SUPERVISION  
*OFFICE ADDRESS:*  
NO 2 OSHOGBO STREET, OGUDU,  
LAGOS STATE

*382* ; 08054178584, 07062539641

### Office stamp

sheet  
content:-

Plan

date :-

sheet no :-

scale :-

1:100

revision :-

Drawn by :-  
Yungola  
Checked by :-  
Oluwaseun

AUGUST, 2024