

PROPOSED RESIDENTIAL DEVELOPMENT

FOR

ADEBAYO OLUWATOBI ABIODUN

**OFF ALAFIATAYO STREET OYALUGBO AREA, ISIA OKEHO,
KAJOLA LOCAL GOVERNMENT AREA,
OYO STATE.**

PREPARED BY



YUNGOLA SERVICES LTD.

**(ARCHITECTURAL DESIGN, STRUCTURAL DESIGN, BUILDING
DEVELOPMENT, PLANNER, SUPERVISION**

ADDRESS;
NO 2 OSHOGBO STREET, OGUDU,
LAGOS STATE

T&L ;
08054178584, 07062539641

DESIGN ;
june1, 2024.

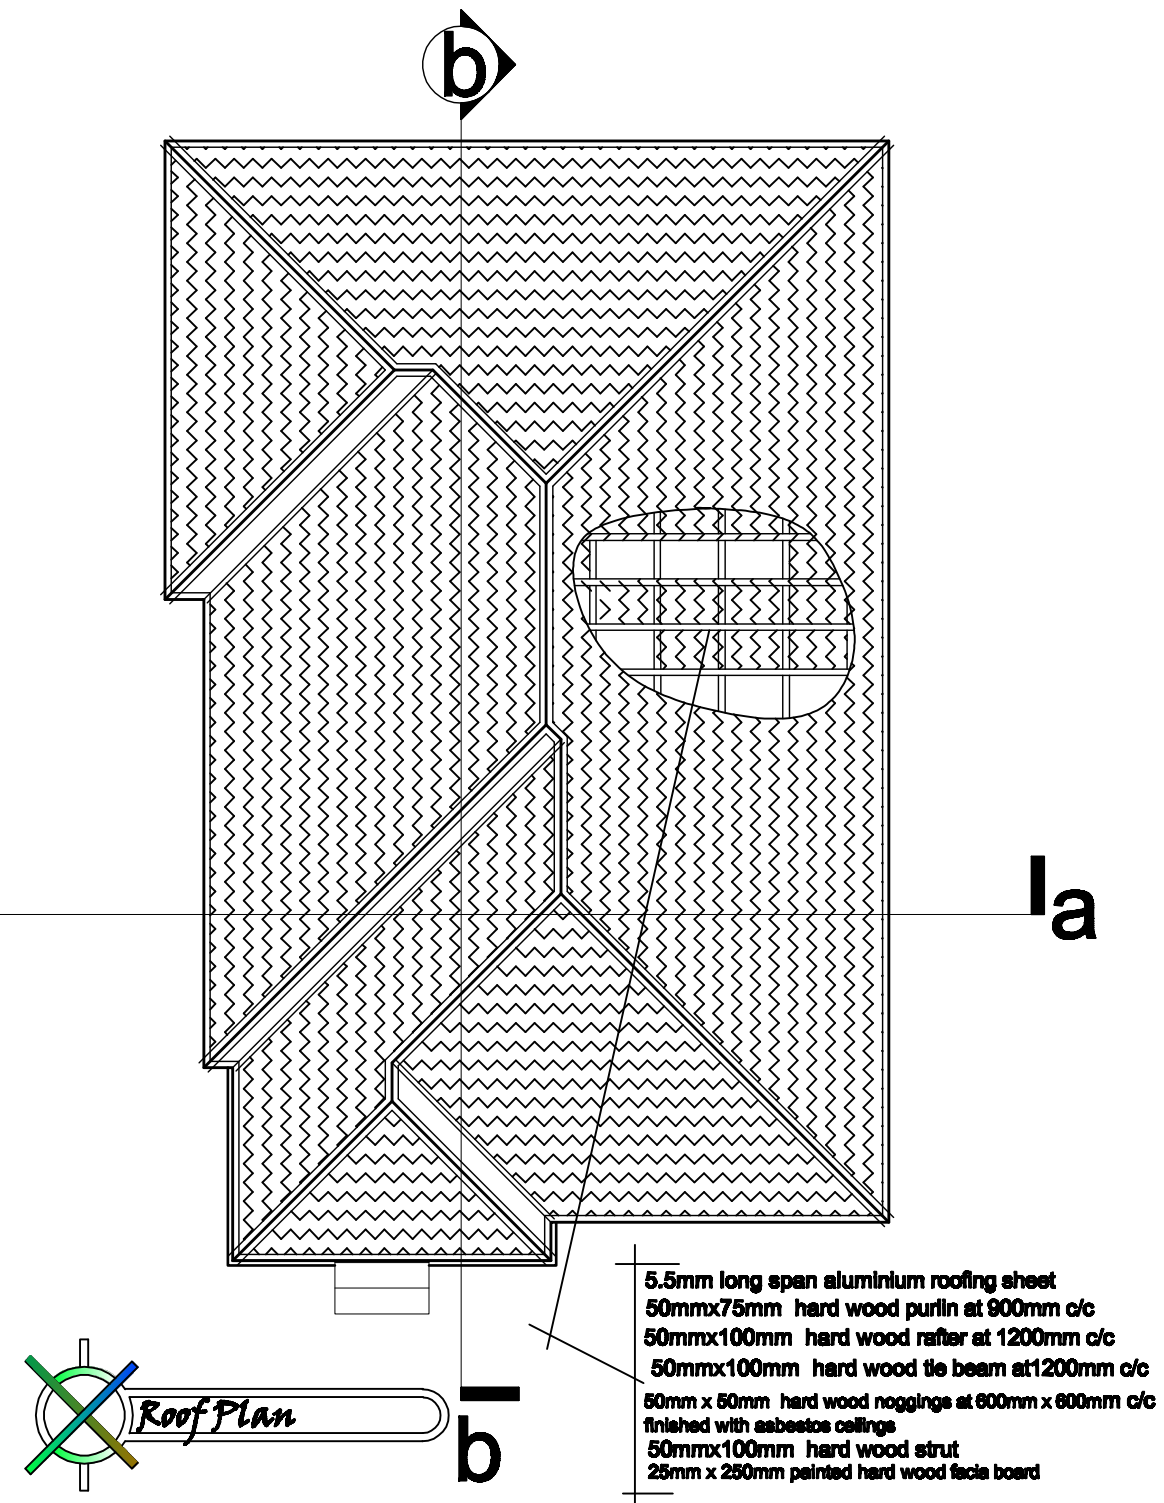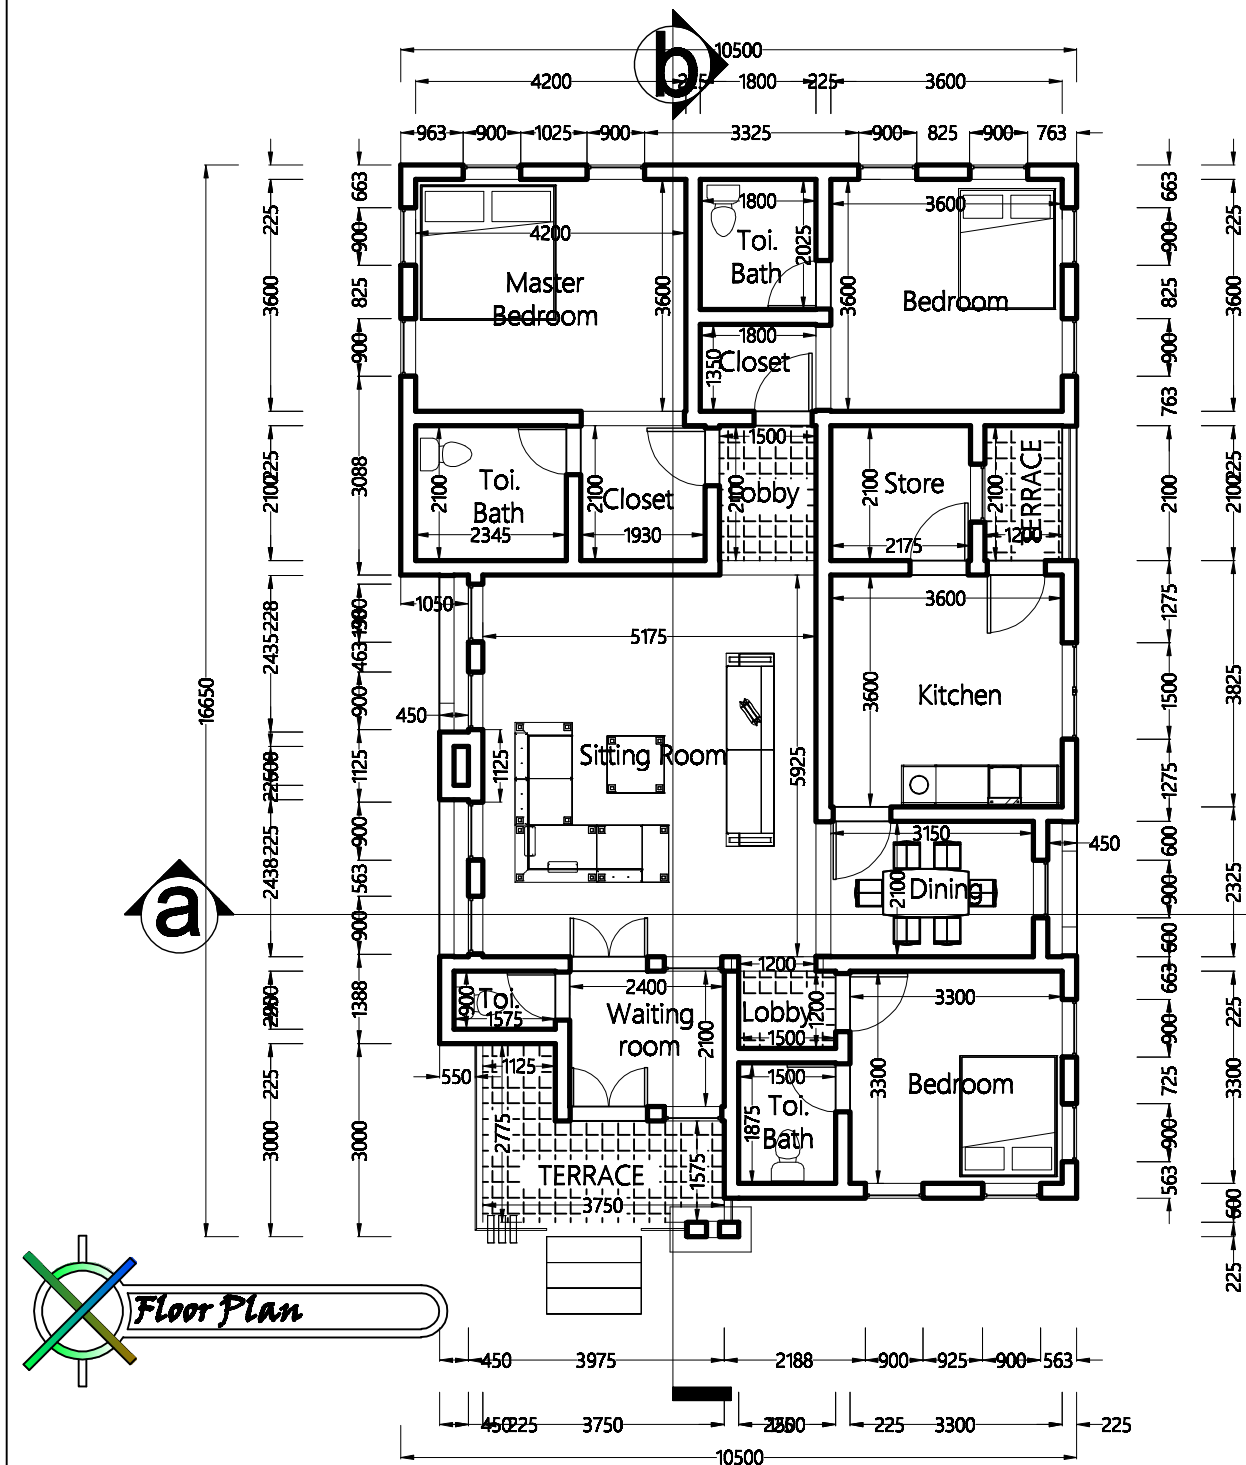

- general note**
- 1) The contractor is to check all the drawing before commencing work.
 - 2) Any discrepancies observed on this drawing issued by any other party are to be immediately brought to consultant Architect Notice.
 - 3) All dimension are in millimeter.
 - 4) Dimension are to be confirmed on site.

Client :-
ADEBAYO OLUWATOBI
ABIODUN

Location :-
OFF ALAFIATAYO STREET OYALUGBO
ATREA, ISIA OKEHO,
KAJOLA LOCAL GOVERNMENT AREA,
OYO STATE.

Project Title :-
Proposed Residential
Development

Working
Drawing

Architect :-
**YUNGOLA SERVICES
LTD.** Rc.1783703
(ARCHITECTURAL DESIGN,
STRUCTURAL DESIGN, BUILDING
DEVELOPMENT, PLANNER,
SUPERVISION

OFFICE ADDRESS:
NO 2 OSHOGBO STREET, OGUDU,
LAGOS STATE

T&L ; 08054178584, 07062539641

Office stamp

sheet content:-
Plan

sheet no.:-


scale :-
1:100

date :-
JUNE, 2024

revision :-

Drawn by :-
Yungola


Checked by :-
Oluwaseun

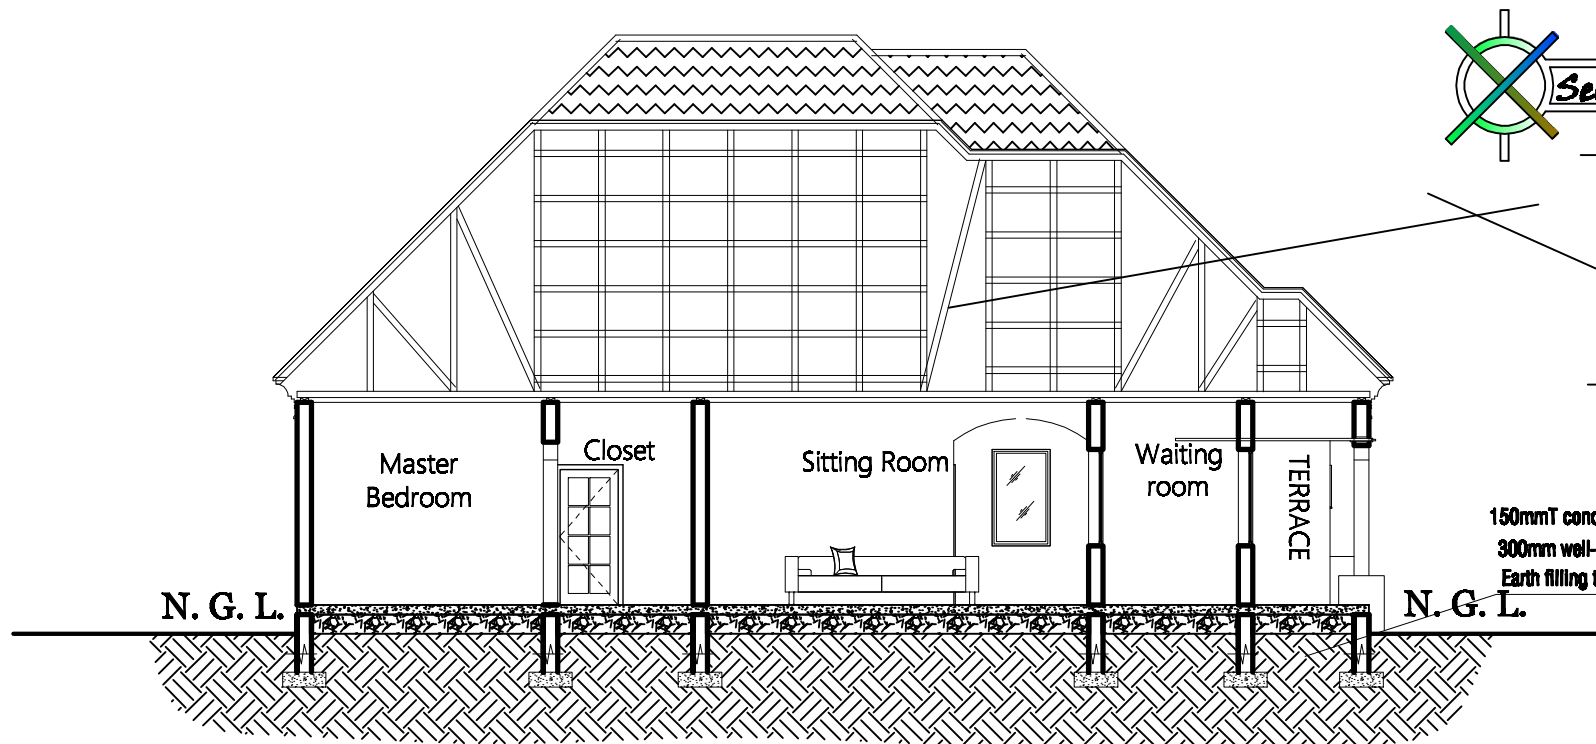

Section b - b

5.5mm long span aluminium roofing sheet
50mmx75mm hard wood purlin at 900mm c/c
50mmx100mm hard wood rafter at 1200mm c/c
50mmx100mm hard wood tie beam at 1200mm c/c
50mm x 50mm hard wood noggings at 600mm x 600mm c/c
finished with asbestos ceilings
50mmx100mm hard wood strut
25mm x 250mm painted hard wood fascia board

150mmT concrete slab over polythene DPM of 50mm blinding
300mm well-compacted Hardcore bed
Earth filling to be well compacted in layers

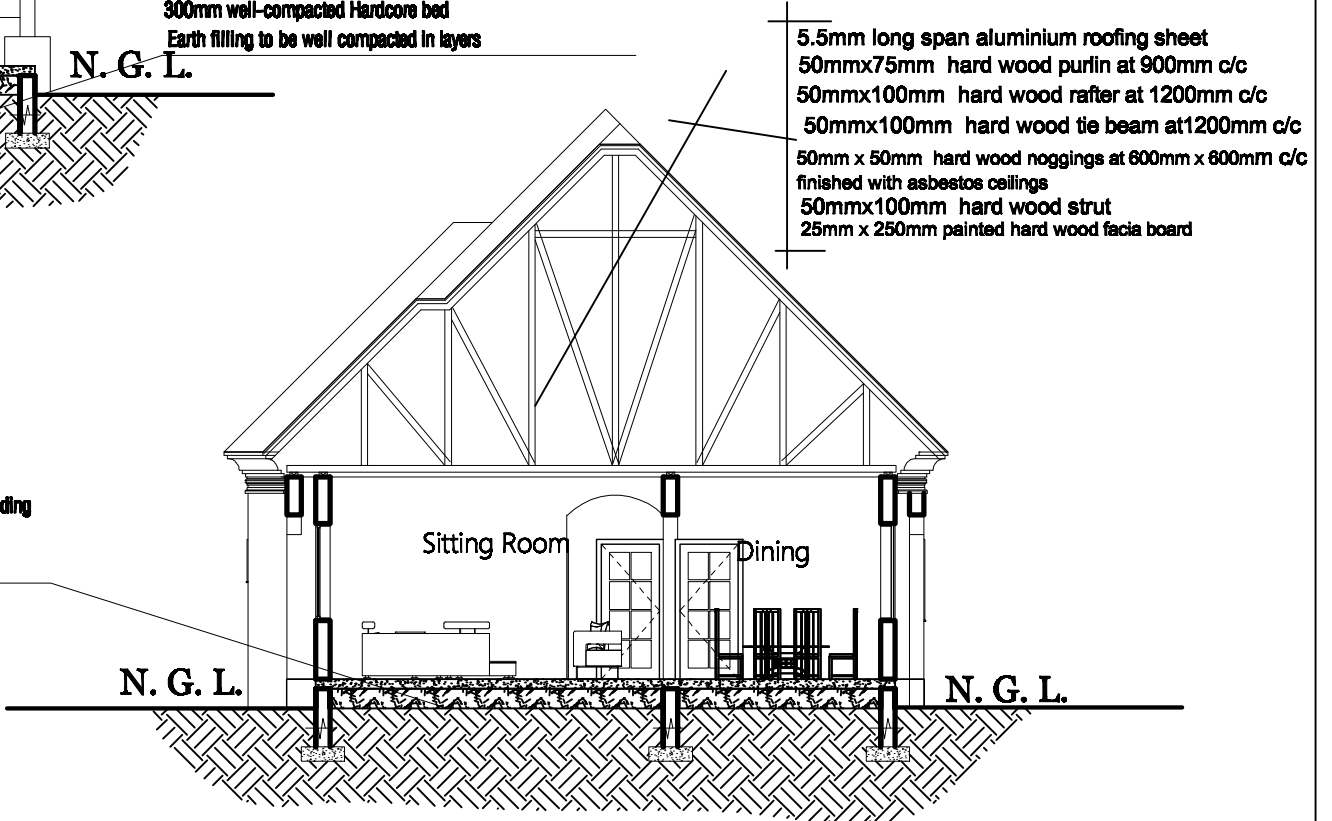

Section a - a

150mmT concrete slab over polythene DPM of 50mm blinding
300mm well-compacted Hardcore bed
Earth filling to be well compacted in layers

general note

- 1) The contractor is to check all the drawing before commencing work.
- 2) Any discrepancies observed on this drawing issued by any other party are to be immediately brought to consultant Architect Notice.
- 3) All dimension are in millimeter.
- 4) Dimension are to be confirmed on site.

Client :-

ADEBAYO OLUWATOBI
ABIODUN

Location :-

OFF ALAFIATAYO STREET OYALUGBO
ATREA, ISIA OKEHO,
KAJOLA LOCAL GOVERNMENT AREA,
OYO STATE.

Project Title :-

Proposed Residential
Development

Working
Drawing

Architect :-

**YUNGOLA SERVICES
LTD.** RC.1783703
(ARCHITECTURAL DESIGN,
STRUCTURAL DESIGN, BUILDING
DEVELOPMENT, PLANNER,
SUPERVISION

OFFICE ADDRESS:

NO 2 OSHOGBO STREET, OGUDU,
LAGOS STATE

T&L ; 08054178584, 07062539641

Office stamp

sheet content:-

Plan

sheet no :-

scale :-

1:100

revision :-

date :-

JUNE, 2024

Drawn by :-
Yungola


Checked by :-
Oluwaseun



Front View



Back View

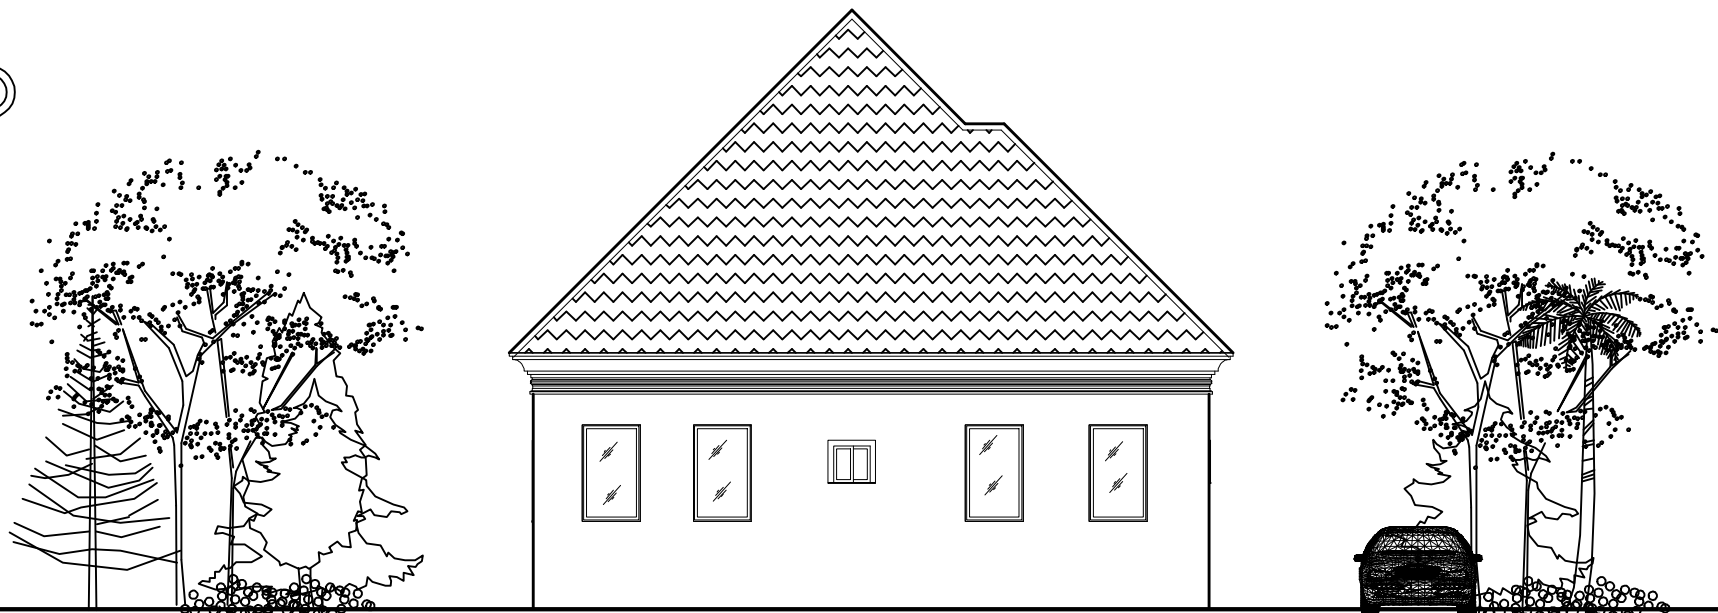

general note

- 1) The contractor is to check all the drawing before commencing work.
- 2) Any discrepancies observed on this drawing issued by any other party are to be immediately brought to consultant Architect Notice.
- 3) All dimension are in millimeter.
- 4) Dimension are to be confirmed on site.

Client :-

ADEBAYO OLUWATOBI
ABIODUN

Location :-

OFF ALAFIATAYO STREET OYALUGBO
ATREA, ISIA OKEHO,
KAJOLA LOCAL GOVERNMENT AREA,
OYO STATE.

Project Title :-

Proposed Residential
Development

Working
Drawing

Architect :-

**YUNGOLA SERVICES
LTD.** RC.1783703
(ARCHITECTURAL DESIGN,
STRUCTURAL DESIGN, BUILDING
DEVELOPMENT, PLANNER,
SUPERVISION

OFFICE ADDRESS:

NO 2 OSHOGBO STREET, OGUDU,
LAGOS STATE

T&L ; 08054178584, 07062539641

Office stamp

sheet content:-

Plan

date :-

JUNE, 2024

sheet no :-

scale :-




1:100

revision :-

Drawn by :-
Yungola

Checked by :-

Oluwaseun

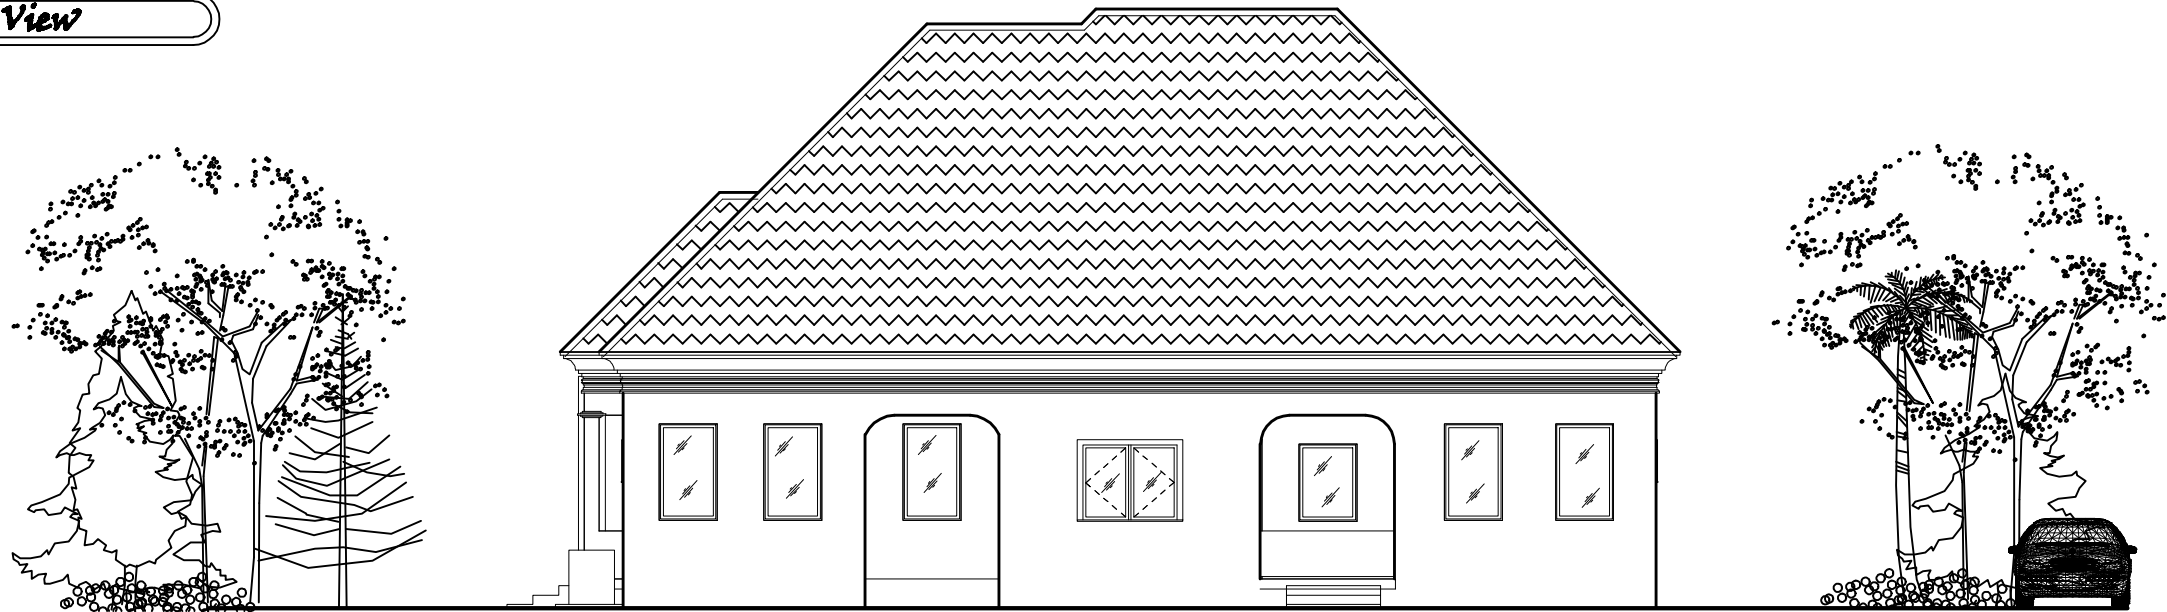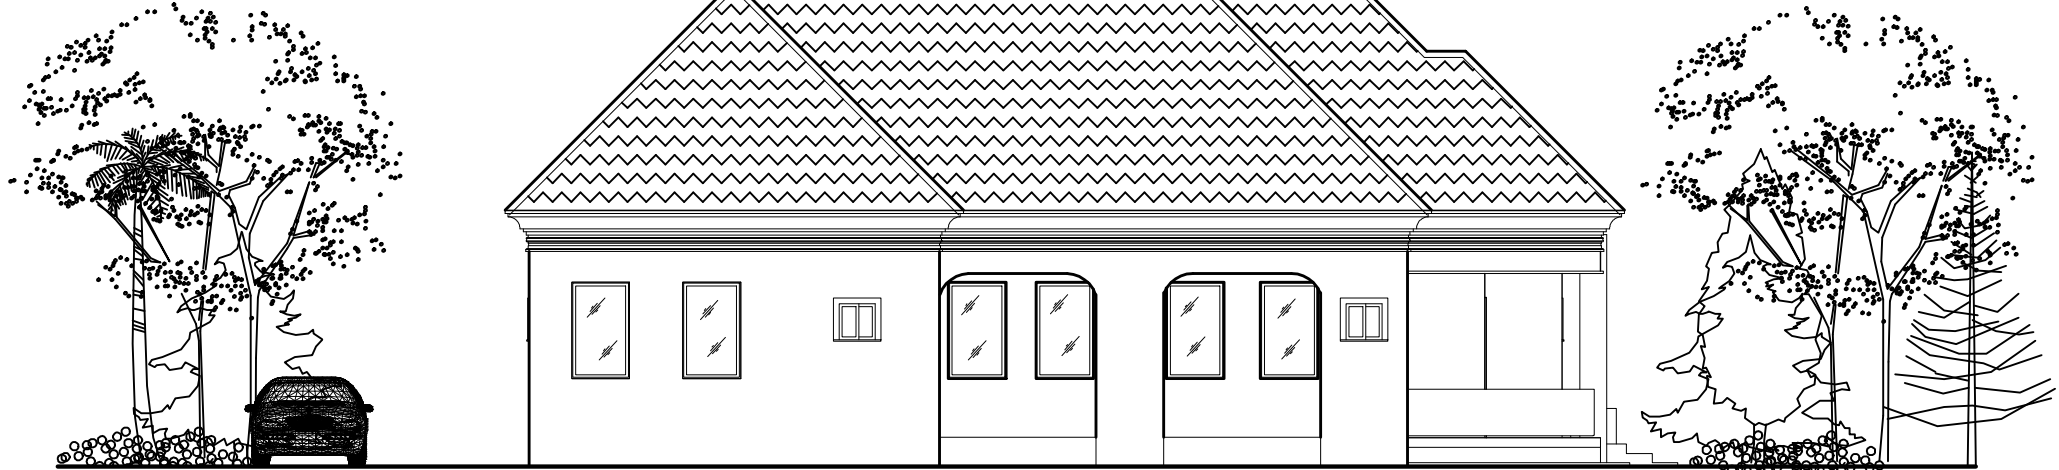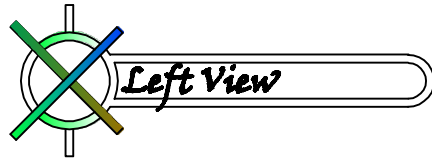

general note

- 1) The contractor is to check all the drawing before commencing work.
- 2) Any discrepancies observed on this drawing issued by any other party are to be immediately brought to consultant Architect Notice.
- 3) All dimension are in millimeter.
- 4) Dimension are to be confirmed on site.

Client :-

ADEBAYO OLUWATOBI
ABIODUN

Location :-

OFF ALAFIATAYO STREET OYALUGBO
ATREA, ISIA OKEHO,
KAJOLA LOCAL GOVERNMENT AREA,
OYO STATE.

Project Title :-

Proposed Residential
Development

Working
Drawing

Architect :-

**YUNGOLA SERVICES
LTD.** RC.1783703
(ARCHITECTURAL DESIGN,
STRUCTURAL DESIGN, BUILDING
DEVELOPMENT, PLANNER,
SUPERVISION

OFFICE ADDRESS:

NO 2 OSHOGBO STREET, OGUDU,
LAGOS STATE

T&L ; 08054178584, 07062539641

Office stamp

sheet content:-

Plan

sheet no :-

scale :-
1:100

revision :-

date :-





JUNE, 2024

Drawn by :-
Yungola

Checked by :-

Oluwaseun

WINDOWS SCHEDULE				
PROFILE				
LABEL ON PLAN	W1	W2	W3	
NO'S REQD	1	11	3	
DESCRIPTION	Aluminum casement windows with burglary bars, fly and mosquito screen			
DIMENSION (MM)	900 X 900	1200 X 1200	600 X 600	

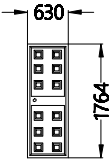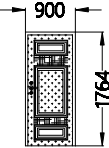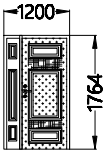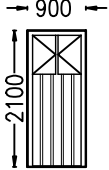DOORS SCHEDULE				
PROFILE				
LABEL ON PLAN	W1	W2	W3	W4
NO'S REQD	3	1	1	5
DESCRIPTION	Single action, single leaf steel panel door with steel frame see manufacturers fixing catalogue for details.	Single action, single leaf steel panel door with steel frame see manufacturers fixing catalogue for details.	Double action, double leaf steel panel security door with steel frame, see manufacturers fixing catalogue for details.	Single action, single leaf steel panel door with steel frame see manufacturers fixing catalogue for details.
DIMENSION (MM)	750 X 2100	900 X 2100	1200 X 2100	900 X 2100



general note

1) The contractor is to check all the drawing before commencing work.
2) Any discrepancies observed on this drawing issued by any other party are to be immediately brought to consultant Architect Notice.
3) All dimension are in millimeter.
4) Dimension are to be confirmed on site.

Client :-
ADEBAYO OLUWATOBI
ABIODUN

Location :-
OFF ALAFIATAYO STREET OYALUGBO
ATREA, ISIA OKEHO,
KAJOLA LOCAL GOVERNMENT AREA,
OYO STATE.

Project Title :-

Proposed Residential
Development

Working
Drawing

Architect :-
**YUNGOLA SERVICES
LTD.** Re.1783703
(ARCHITECTURAL DESIGN,
STRUCTURAL DESIGN, BUILDING
DEVELOPMENT, PLANNER,
SUPERVISION
OFFICE ADDRESS:
NO 2 OSHOGBO STREET, OGUDU,
LAGOS STATE
T&L ; 08054178584, 07062539641

Office stamp

sheet content:-
Plan

sheet no :-

scale :-
1:100

date :-
JUNE, 2024

revision :-

Drawn by :-
Yungola

Checked by :-
Oluwaseun

Drawn by:- Yungola
Checked by:- Oluwaseun