

PROPOSED RESIDENTIAL DEVELOPMENT

FOR

**SURV. SHITTABEY SIRAJDEEN
OLABODE**

AT AYOBO LOW INCOME RESIDENTIAL SCHEME, SUBDIVISION OF PLOT 15, BLOCK 8, AREA (15B)
ALIMOSHO LOCAL AREA, OYOBO,
LAGOS STATE.

PREPARED BY

YUNGOLA SERVICES LTD.


**(ARCHITECTURAL DESIGN, STRUCTURAL DESIGN, BUILDING
DEVELOPMENT, PLANNER, SUPERVISION**

ADDRESS;
NO 2 OSHOGBO STREET, OGUDU,
LAGOS STATE

T&L ;
08054178584, 07062539641

DESIGN ;
Mayl, 2024.

SITE PLAN

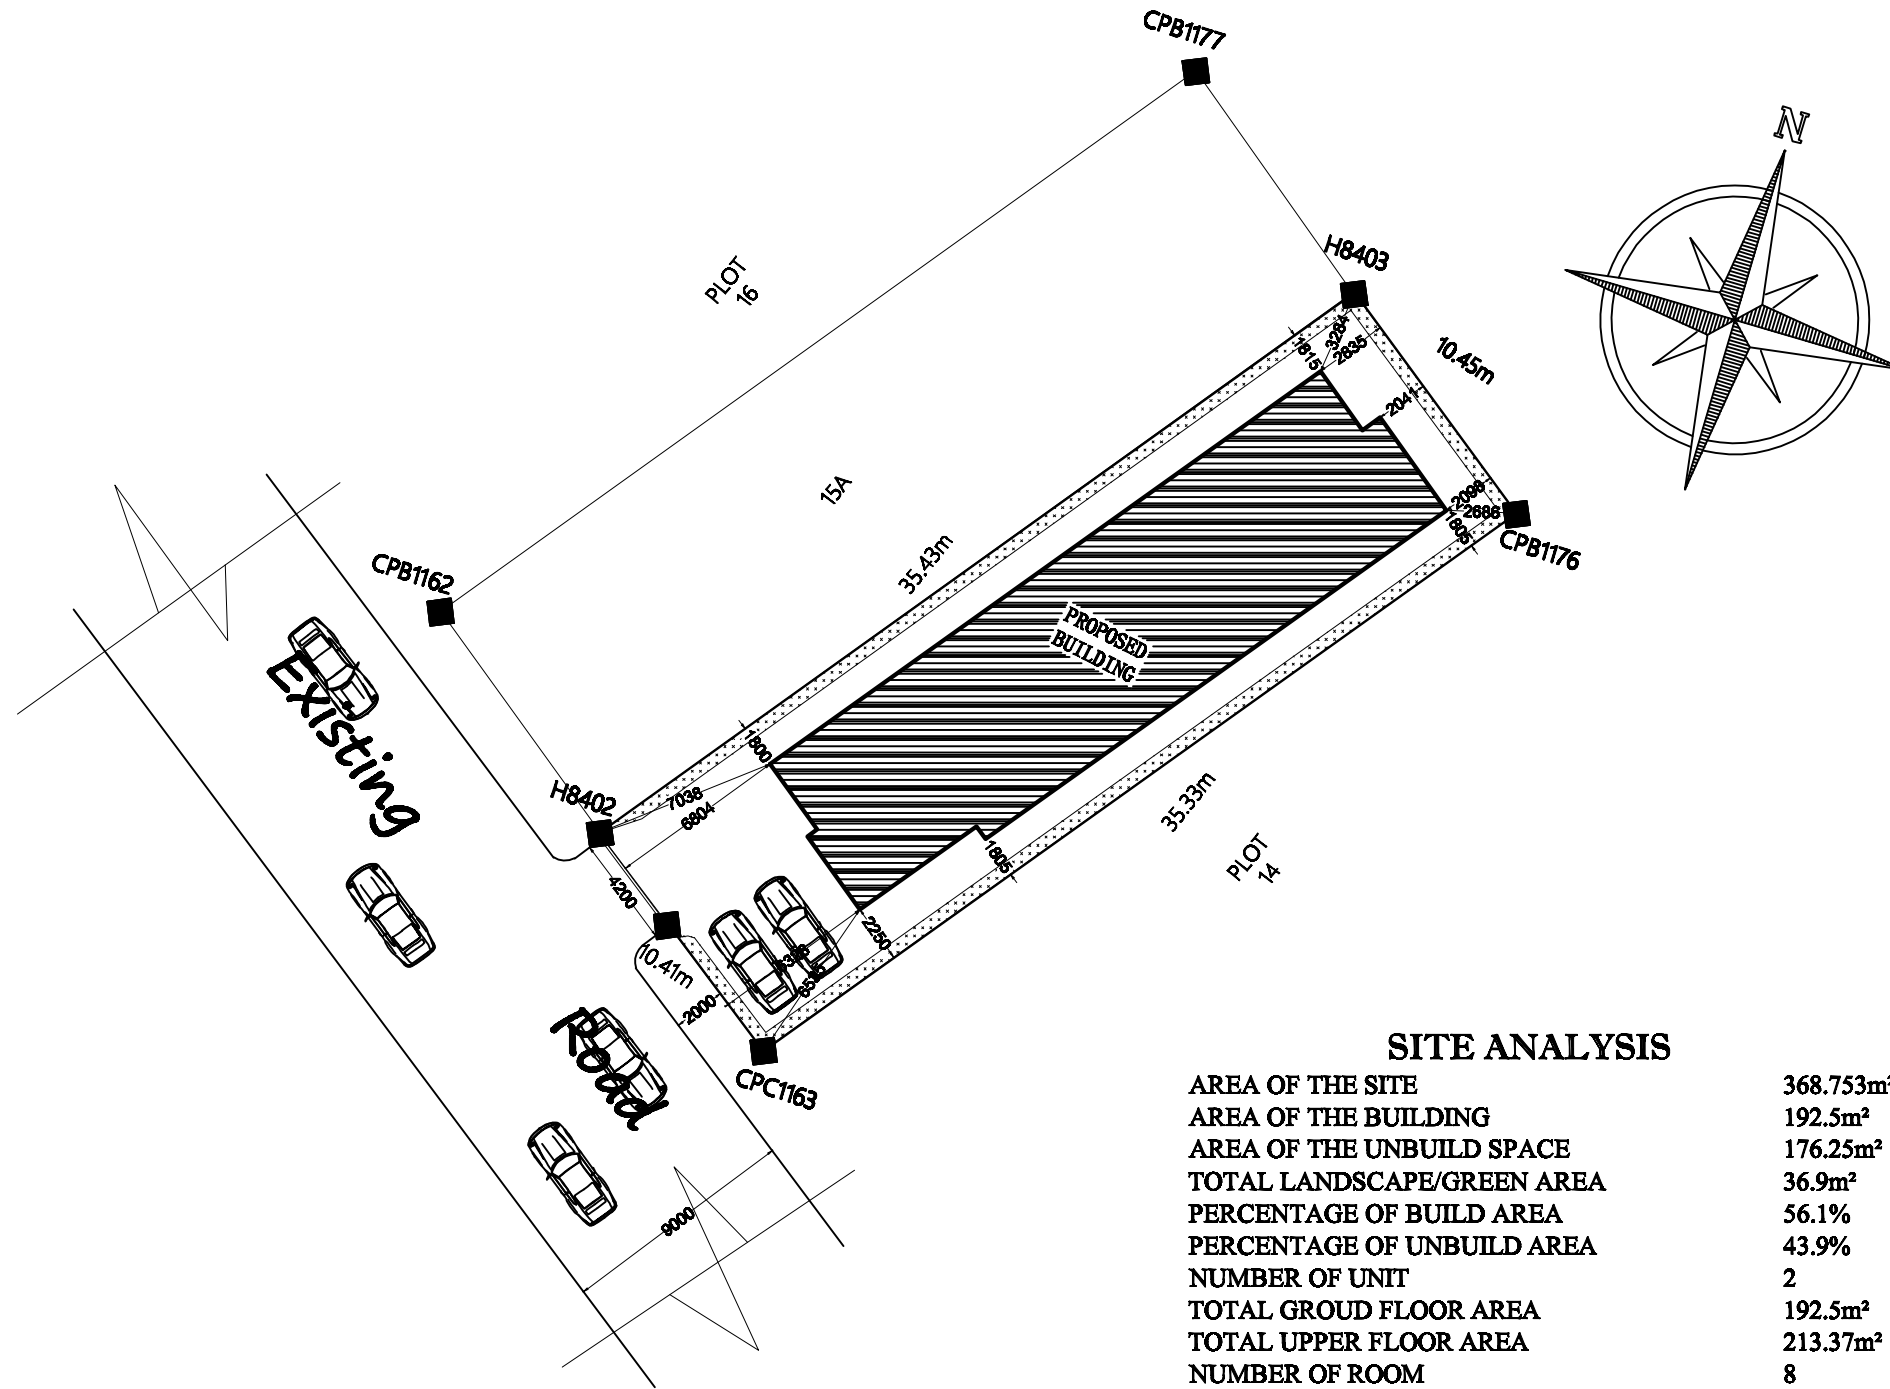

SITE ANALYSIS

AREA OF THE SITE	368.753m ²
AREA OF THE BUILDING	192.5m ²
AREA OF THE UNBUILD SPACE	176.25m ²
TOTAL LANDSCAPE/GREEN AREA	36.9m ²
PERCENTAGE OF BUILD AREA	56.1%
PERCENTAGE OF UNBUILD AREA	43.9%
NUMBER OF UNIT	2
TOTAL GROUND FLOOR AREA	192.5m ²
TOTAL UPPER FLOOR AREA	213.37m ²
NUMBER OF ROOM	8
NUMBER OF FLOOR	2

NOTE;

general note

- 1) The contractor is to check all the drawing before commencing work.
- 2) Any discrepancies observed on this drawing issued by any other party are to be immediately brought to consultant Architect Notice.
- 3) All dimension are in millimeter.
- 4) Dimension are to be confirmed on site.

Client :-

SURV. SHITTABEY SIRAJDEEN
OLABODE

Location :-

AT AYOBO LOW INCOME RESIDENTIAL
SCHEME, SUBDIVISION OF PLOT 15,
BLOCK 8, AREA (15B)

ALIMOSHO LOCAL AREA, OYOBO,
LAGOS STATE.

Project Title :-

Proposed Residential
Development

Working
Drawing

Architect :-

**YUNGOLA SERVICES
LTD.** RC.1783703
(ARCHITECTURAL DESIGN,
STRUCTURAL DESIGN, BUILDING
DEVELOPMENT, PLANNER,
SUPERVISION

OFFICE ADDRESS:

NO 2 OSHOGBO STREET, OGUDU,
LAGOS STATE

T&L ; 08054178584, 07062539641

Office stamp

sheet content:-

Plan

date :-

MAY, 2024

sheet no :-

scale :-


1:100

revision :-

Drawn by :-
Yungola

Checked by :-
Oluwaseun

NOTE;

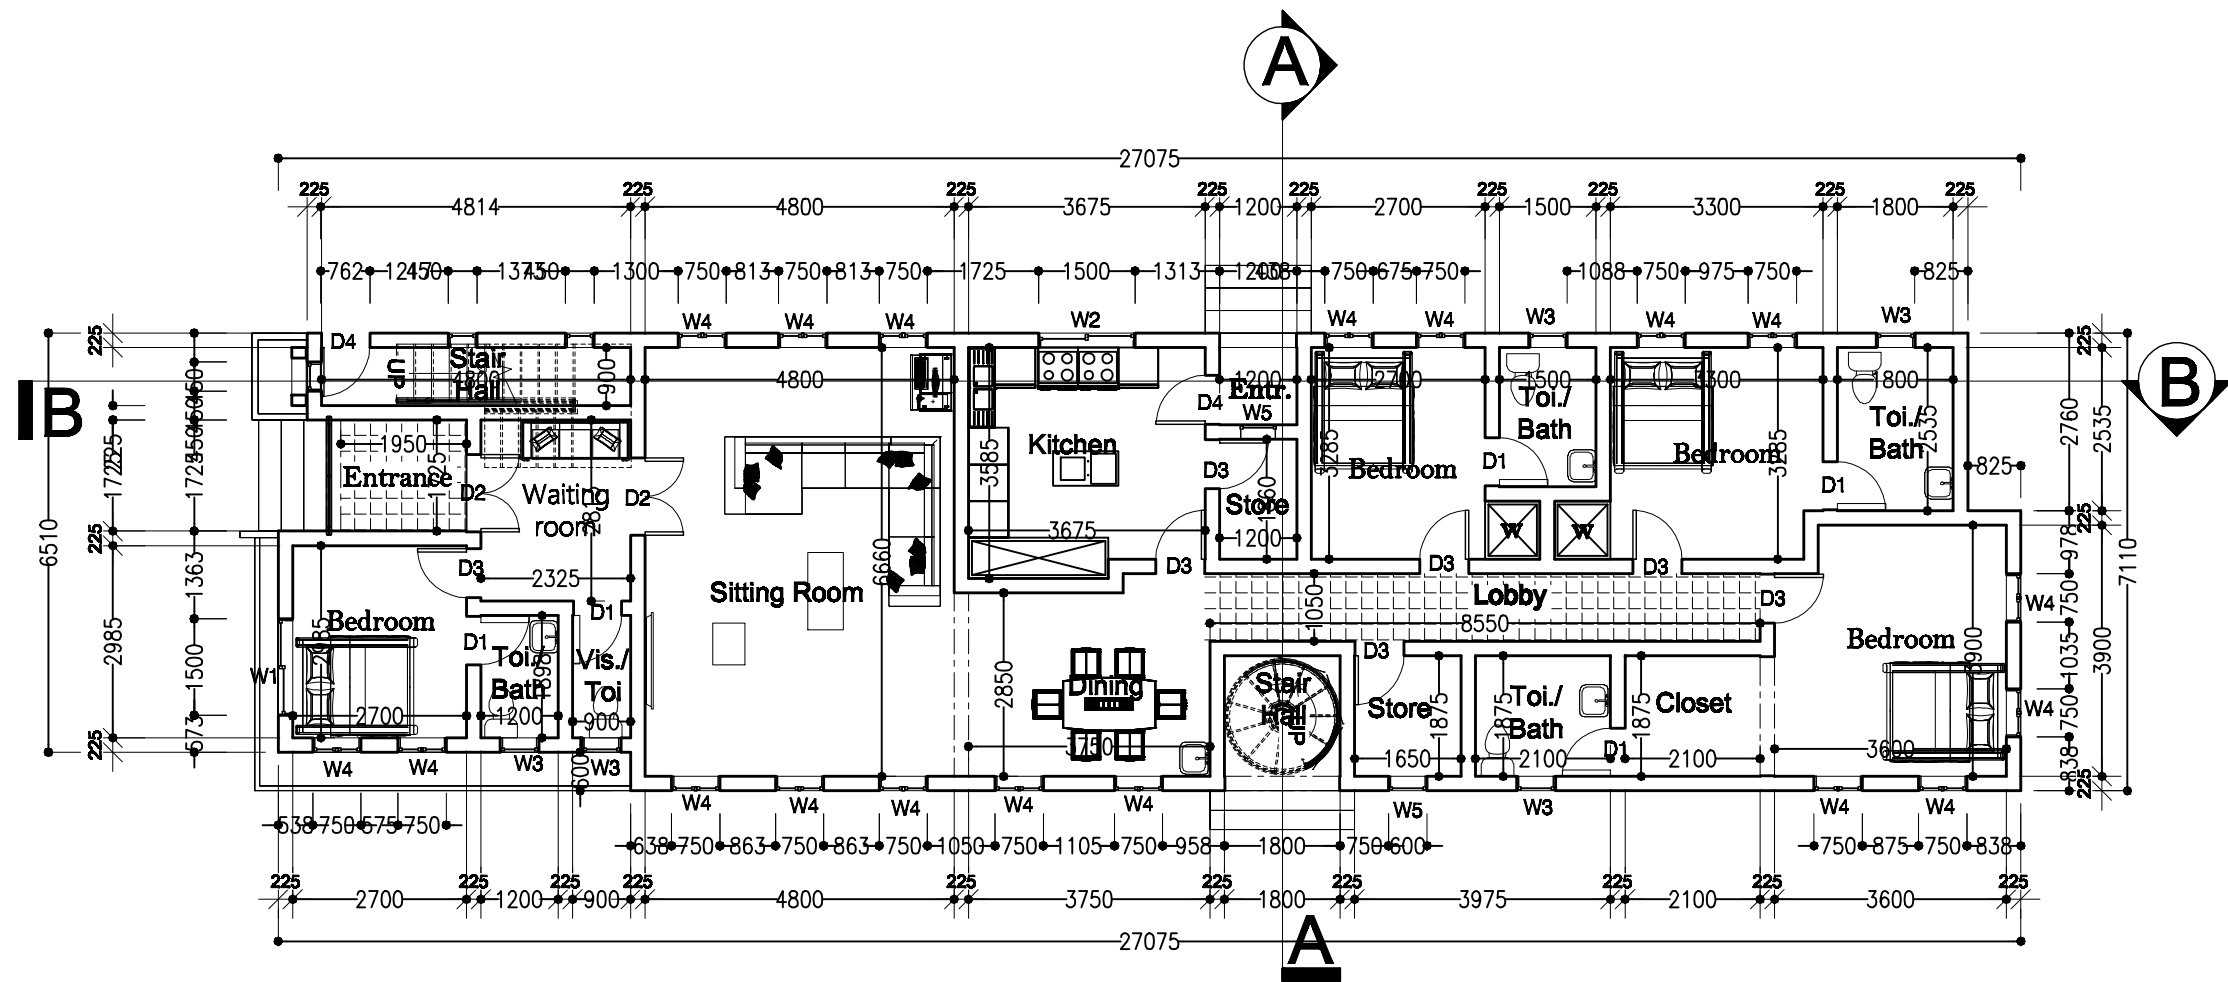

GROUND FLOOR PLAN

general note

- 1) The contractor is to check all the drawing before commencing work.
- 2) Any discrepancies observed on this drawing issued by any other party are to be immediately brought to consultant Architect Notice.
- 3) All dimension are in millimeter.
- 4) Dimension are to be confirmed on site.

Client :-

SURV. SHITTABEY SIRAJDEEN
OLABODE

Location :-

AT AYOBO LOW INCOME RESIDENTIAL
SCHEME, SUBDIVISION OF PLOT 15,
BLOCK 8, AREA (158)

ALIMOSHO LOCAL AREA, OYOBO,
LAGOS STATE.

Project Title :-

Proposed Residential
Development

Working
Drawing

Architect :-

**YUNGOLA SERVICES
LTD.** RC.1783703
(ARCHITECTURAL DESIGN,
STRUCTURAL DESIGN, BUILDING
DEVELOPMENT, PLANNER,
SUPERVISION

OFFICE ADDRESS:

NO 2 OSHOGBO STREET, OGUDU,
LAGOS STATE

T&L ; 08054178584, 07062539641

Office stamp

sheet content:-

Plan

date :-

MAY, 2024


sheet no. :-

scale :-

1:100

revision :-

Drawn by :-
Yungola
Checked by :-
Oluwaseun

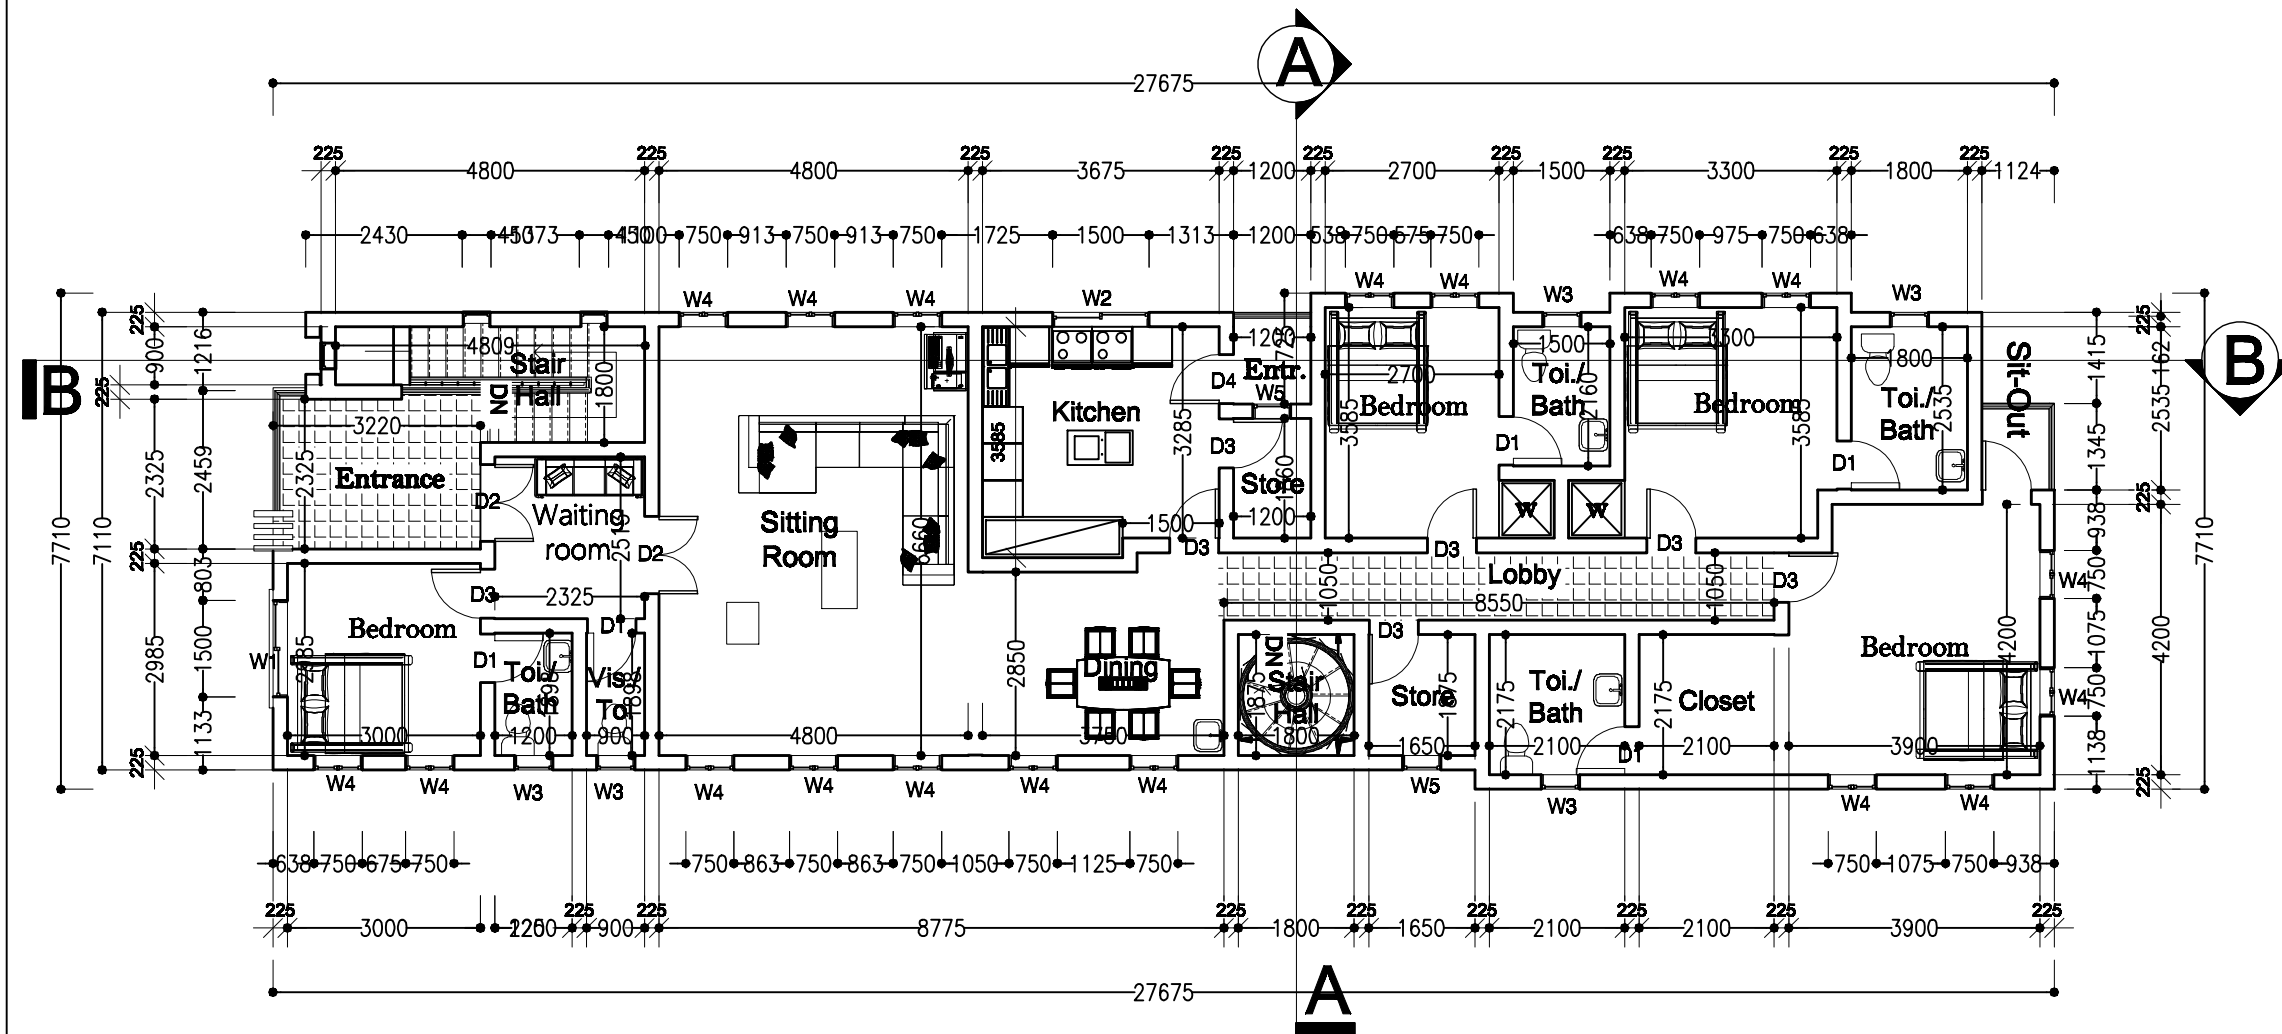

NOTE;

UPPER FLOOR PLAN

general note

- 1) The contractor is to check all the drawing before commencing work.
- 2) Any discrepancies observed on this drawing issued by any other party are to be immediately brought to consultant Architect Notice.
- 3) All dimension are in millimeter.
- 4) Dimension are to be confirmed on site.

Client :-
SURV. SHITTABEY SIRAJDEEN
OLABODE

Location :-
AT AYOBO LOW INCOME RESIDENTIAL
SCHEME, SUBDIVISION OF PLOT 15,
BLOCK 8, AREA (15B)
ALIMOSHO LOCAL AREA, OYOBO,
LAGOS STATE.

Project Title :-

Proposed Residential
Development

Working
Drawing

Architect :-

**YUNGOLA SERVICES
LTD.** RC.1783703
(ARCHITECTURAL DESIGN,
STRUCTURAL DESIGN, BUILDING
DEVELOPMENT, PLANNER,
SUPERVISION

OFFICE ADDRESS:

NO 2 OSHOGBO STREET, OGUDU,
LAGOS STATE

T&L ; 08054178584, 07062539641

Office stamp

sheet content:-

Plan

date :-

MAY, 2024


sheet no. :-

scale :-

1:100

revision :-

Drawn by :-
Yungola
Checked by :-
Oluwaseun

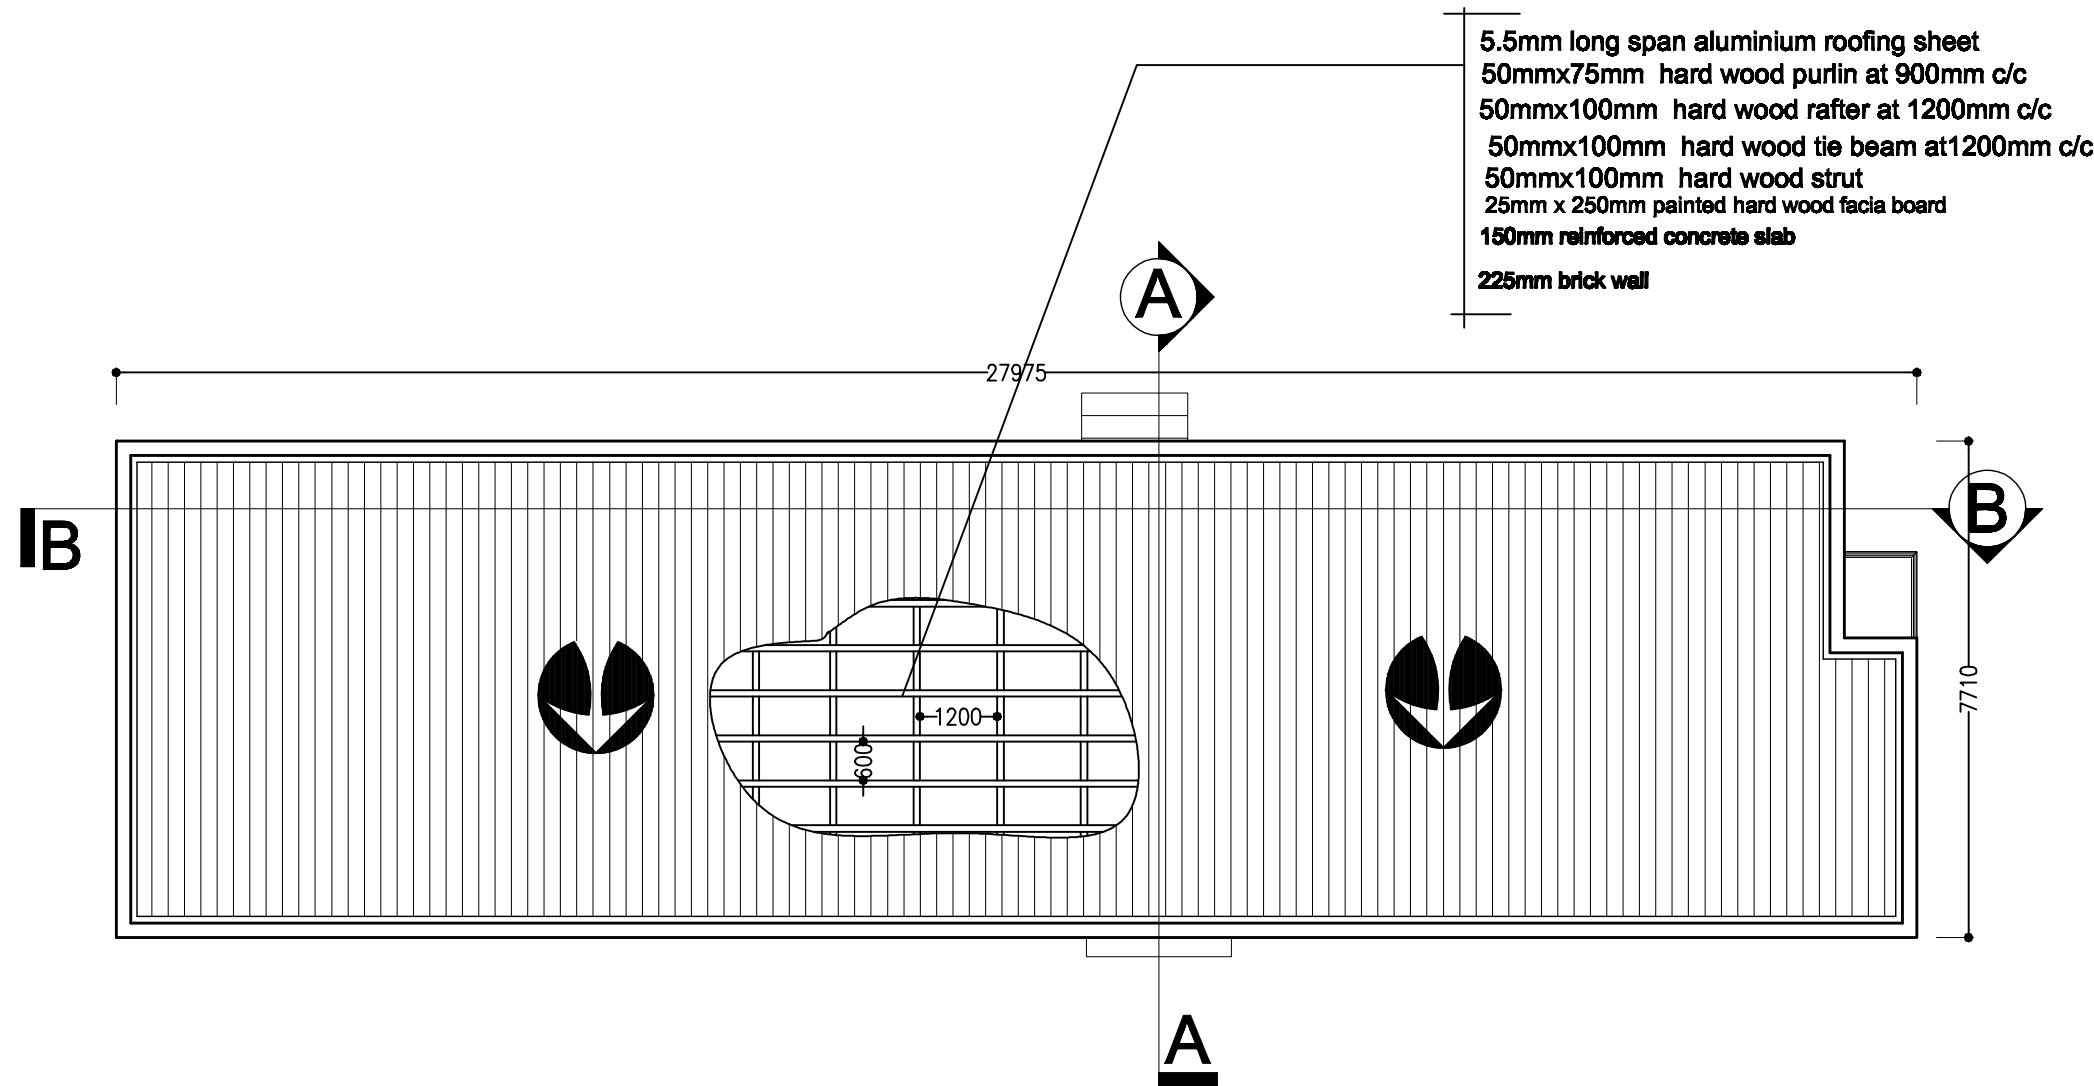

NOTE;

ROOF PLAN

general note

- 1) The contractor is to check all the drawing before commencing work.
- 2) Any discrepancies observed on this drawing issued by any other party are to be immediately brought to consultant Architect Notice.
- 3) All dimension are in millimeter.
- 4) Dimension are to be confirmed on site.

Client :-

SURV. SHITTABEY SIRAJDEEN
OLABODE

Location :-

AT AYOBO LOW INCOME RESIDENTIAL
SCHEME, SUBDIVISION OF PLOT 15,
BLOCK 8, AREA (158)

ALIMOSHO LOCAL AREA, OYOBO,
LAGOS STATE.

Project Title :-

Proposed Residential
Development

Working
Drawing

Architect :-

**YUNGOLA SERVICES
LTD.** Re.1783703
(ARCHITECTURAL DESIGN,
STRUCTURAL DESIGN, BUILDING
DEVELOPMENT, PLANNER,
SUPERVISION

OFFICE ADDRESS:

NO 2 OSHOGBO STREET, OGUDU,
LAGOS STATE

T&L ; 08054178584, 07062539641

Office stamp

sheet content:-

Plan

sheet no :-

scale :-

1:100

revision :-


date :-

MAY, 2024

Drawn by :-
Yungola

Checked by :-


Oluwaseun

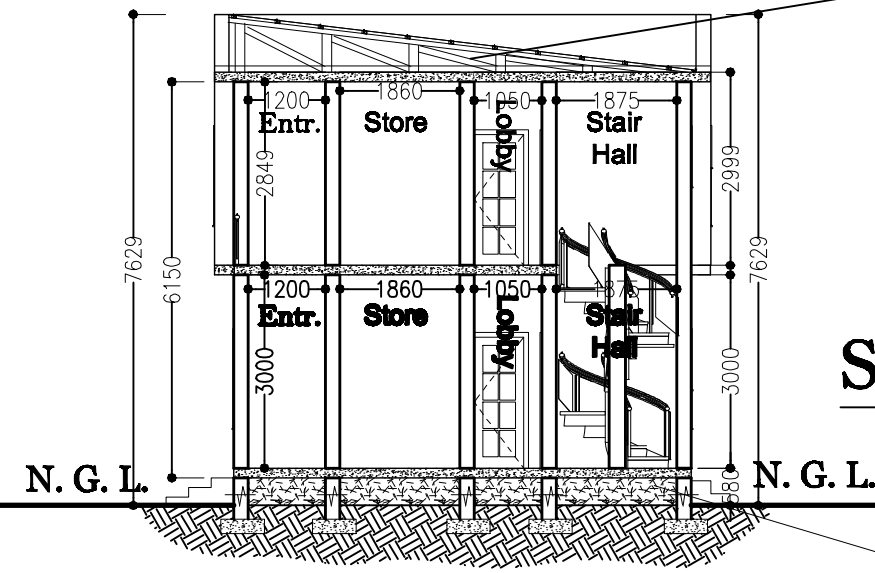

SECTION A-A

- 5.5mm long span aluminium roofing sheet
50mmx75mm hard wood purlin at 900mm c/c
50mmx100mm hard wood rafter at 1200mm c/c
50mmx100mm hard wood tie beam at 1200mm c/c
50mmx100mm hard wood strut
25mm x 250mm painted hard wood facia board
150mm reinforced concrete slab

NOTE;

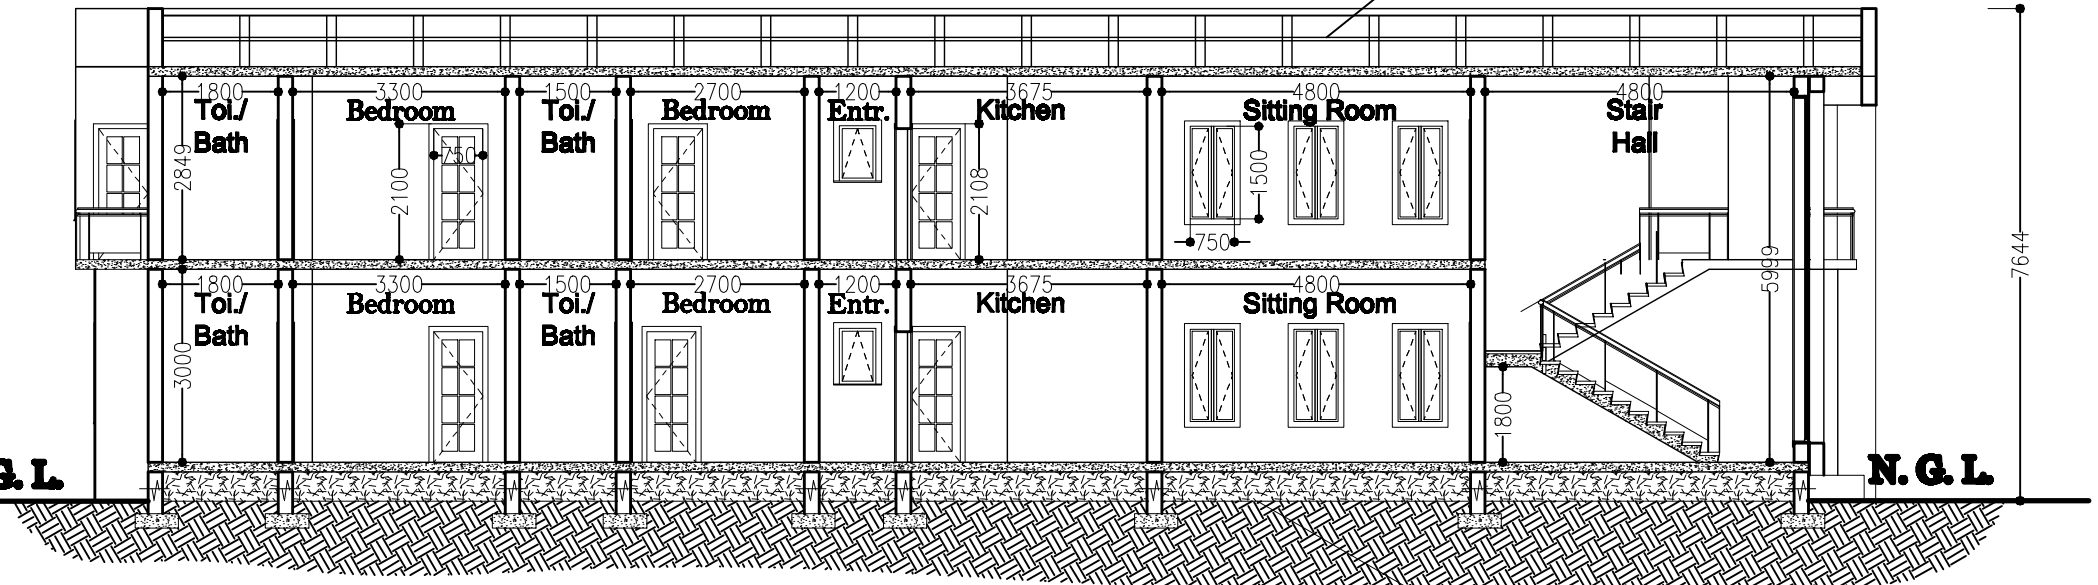

SECTION B-B

150mmT concrete slab over polythene DPM of 50mm blinding
300mm well-compacted Hardcore bed
Earth filling to be well compacted in layers

general note

- 1) The contractor is to check all the drawing before commencing work.
- 2) Any discrepancies observed on this drawing issued by any other party are to be immediately brought to consultant Architect Notice.
- 3) All dimension are in millimeter.
- 4) Dimension are to be confirmed on site.

Client :-
SURV. SHITTABEY SIRAJDEEN
OLABODE

Location :-
AT AYOBO LOW INCOME RESIDENTIAL
SCHEME, SUBDIVISION OF PLOT 15,
BLOCK 8, AREA (15B)

ALIMOSHO LOCAL AREA, OYOBO,
LAGOS STATE.

Project Title :-

Proposed Residential
Development

Working
Drawing

Architect :-
**YUNGOLA SERVICES
LTD.** RC.1783703
(ARCHITECTURAL DESIGN,
STRUCTURAL DESIGN, BUILDING
DEVELOPMENT, PLANNER,
SUPERVISION
OFFICE ADDRESS:
NO 2 OSHOGBO STREET, OGUDU,
LAGOS STATE
T&L ; 08054178584, 07062539641

Office stamp

sheet content:-	sheet no. :-
Plan	scale :-
date :-	revision :-
MAY, 2024	Drawn by :- Yungola Checked by :- Oluwaseun



FRONT VIEW

NOTE;



BACK VIEW

general note
1) The contractor is to check all the drawing before commencing work.
2) Any discrepancies observed on this drawing issued by any other party are to be immediately brought to consultant Architect Notice.
3) All dimension are in millimeter.
4) Dimension are to be confirmed on site.

Client :-
SURV. SHITTABEY SIRAJDEEN
OLABODE
Location :-
AT AYOBO LOW INCOME RESIDENTIAL SCHEME, SUBDIVISION OF PLOT 15, BLOCK 8, AREA (158)
ALIMOSHO LOCAL AREA, OYOBO, LAGOS STATE.

Project Title :-
Proposed Residential Development

Working Drawing

Architect :-
YUNGOLA SERVICES LTD. *Re.1783703*
(ARCHITECTURAL DESIGN, STRUCTURAL DESIGN, BUILDING DEVELOPMENT, PLANNER, SUPERVISION)
OFFICE ADDRESS:
NO 2 OSHOGBO STREET, OGUDU, LAGOS STATE
T&L ; 08054178584, 07062539641


Office stamp

sheet content:-	sheet no :-
Plan	
date :-	revision :-
MAY, 2024	


scale :- 1:100

Drawn by :- Yungola

Checked by :- Oluwaseun

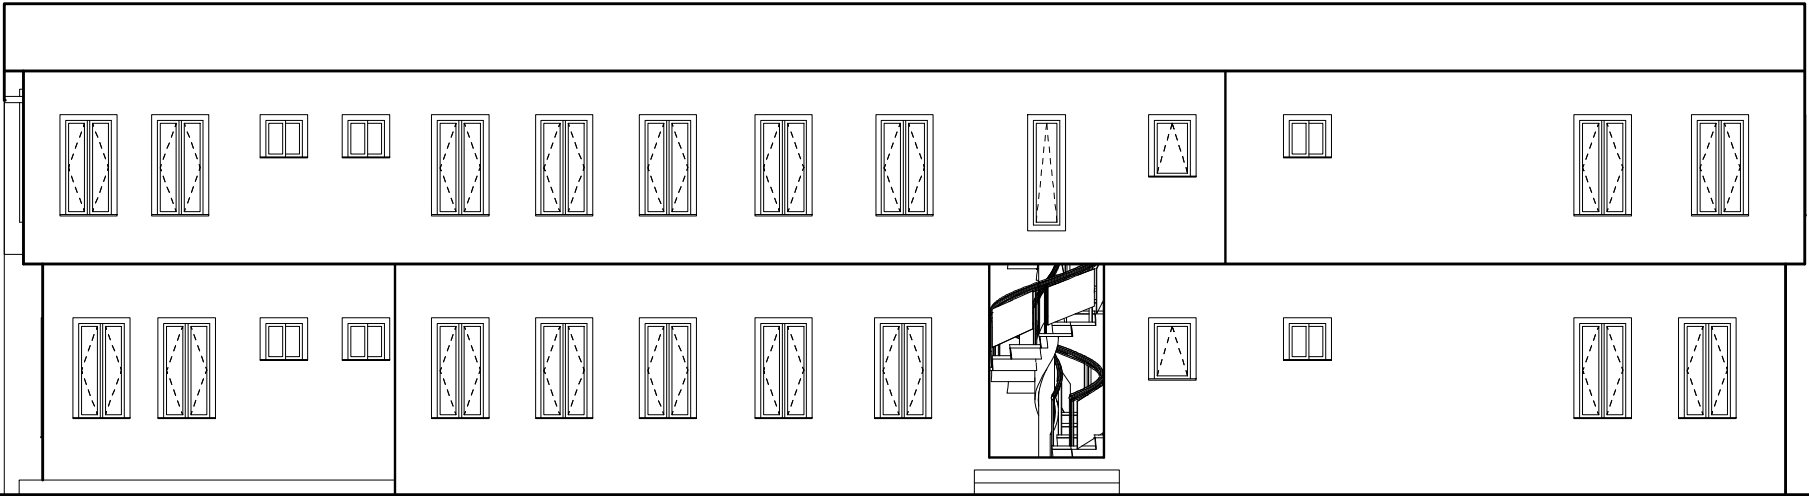

RIGHT VIEW

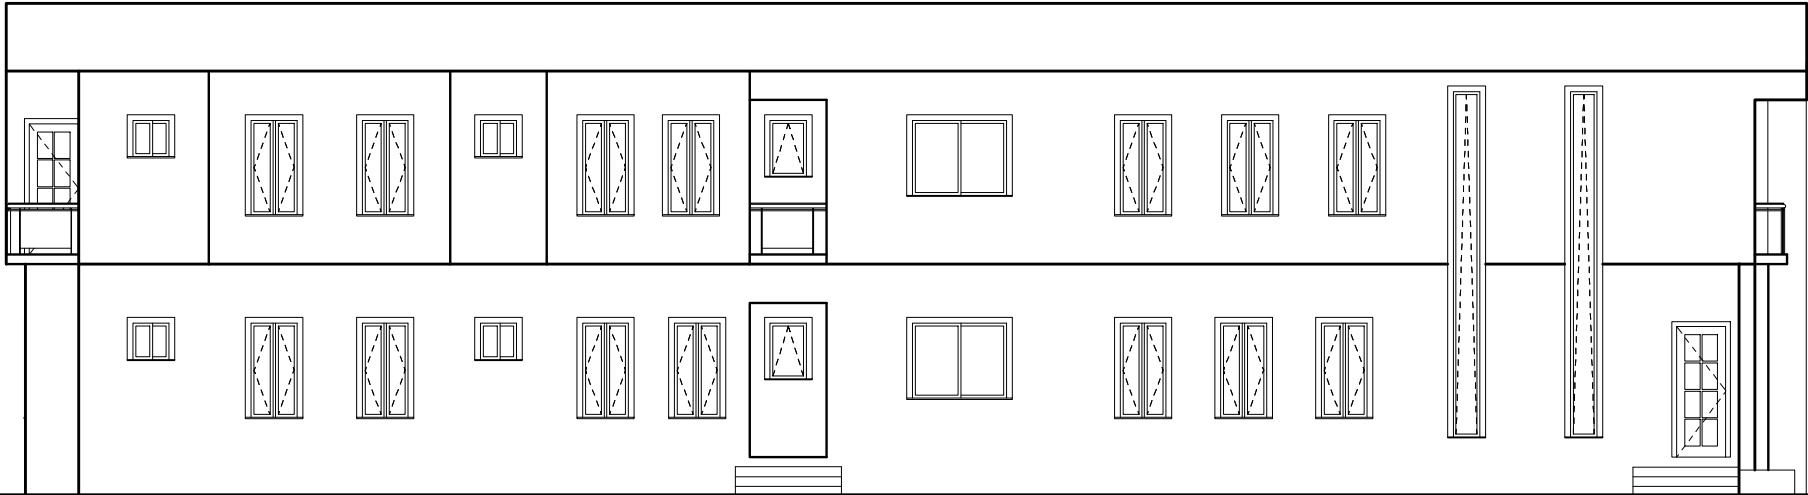

LEFT VIEW

NOTE;

general note

- 1) The contractor is to check all the drawing before commencing work.
- 2) Any discrepancies observed on this drawing issued by any other party are to be immediately brought to consultant Architect Notice.
- 3) All dimension are in millimeter.
- 4) Dimension are to be confirmed on site.

Client :-
SURV. SHITTABEY SIRAJDEEN
OLABODE

Location :-
AT AYOBO LOW INCOME RESIDENTIAL
SCHEME, SUBDIVI SION OF PLOT 15,
BLOCK 8, AREA (158)

ALIMOSHO LOCAL AREA, OYOBO,
LAGOS STATE.

Project Title :-

Proposed Residential
Development

Working
Drawing

Architect :-
**YUNGOLA SERVICES
LTD.** Re.1783703
(ARCHITECTURAL DESIGN,
STRUCTURAL DESIGN, BUILDING
DEVELOPMENT, PLANNER,
SUPERVISION
OFFICE ADDRESS;
NO 2 OSHOGBO STREET, OGUDU,
LAGOS STATE
T&L ; 08054178584, 07062539641

Office stamp

sheet content:-

Plan

date :-

MAY, 2024

sheet no :-

scale :-

1:100


revision :-

Drawn by :-
Yungola

Checked by :-
Oluwaseun

FOUNDATION FOOTING

NOTE;

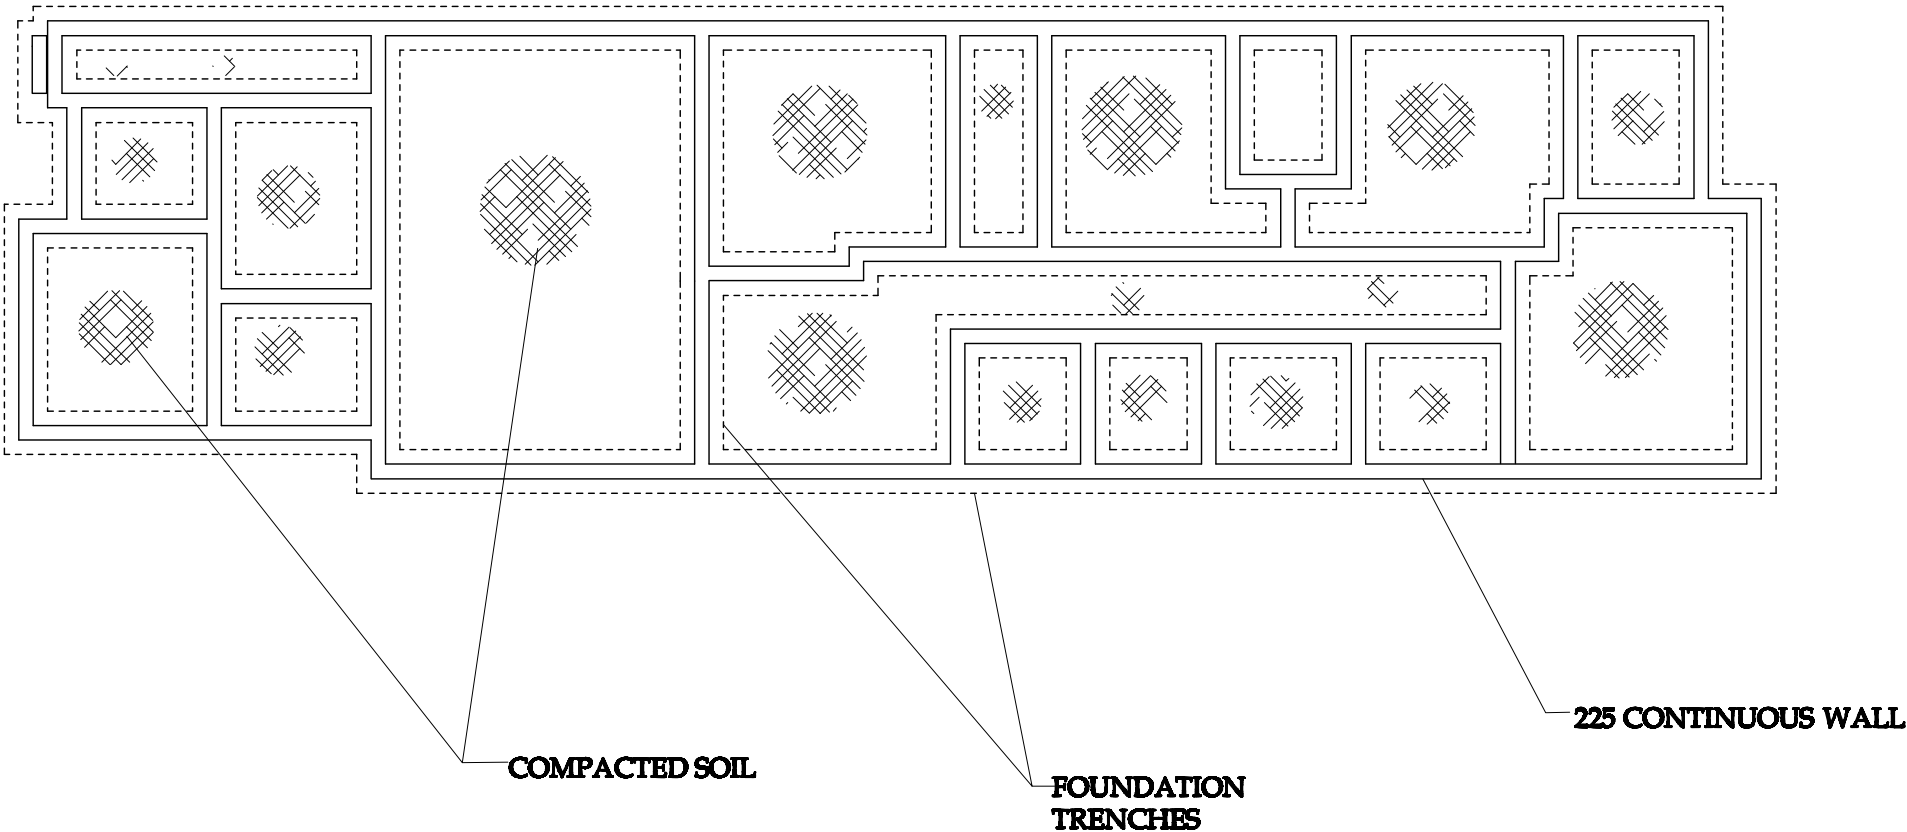

FOUNDATIN
PLAN

general note

- 1) The contractor is to check all the drawing before commencing work.
- 2) Any discrepancies observed on this drawing issued by any other party are to be immediately brought to consultant Architect Notice.
- 3) All dimension are in millimeter.
- 4) Dimension are to be confirmed on site.

Client :-
SURV. SHITTABEY SIRAJDEEN
OLABODE

Location :-
AT AYOBO LOW INCOME RESIDENTIAL
SCHEME, SUBDIVI SION OF PLOT 15,
BLOCK 8, AREA (158)

ALIMOSHO LOCAL AREA, OYOBO,
LAGOS STATE.

Project Title :-

Proposed Residential
Development

Working
Drawing

Architect :-
**YUNGOLA SERVICES
LTD.** Re.1783703
(ARCHITECTURAL DESIGN,
STRUCTURAL DESIGN, BUILDING
DEVELOPMENT, PLANNER,
SUPERVISION
OFFICE ADDRESS:
NO 2 OSHOGBO STREET, OGUDU,
LAGOS STATE
T&L ; 08054178584, 07062539641

Office stamp

sheet content:-

Plan

date :-

MAY, 2024

sheet no. :-







scale :-





1:100

revision :-

Drawn by :-
Yungola

Checked by :-
Oluwaseun

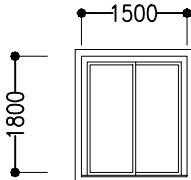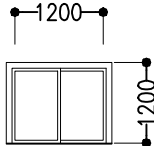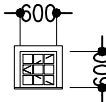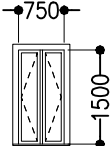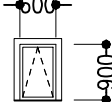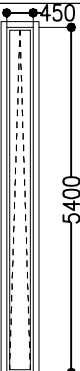WINDOWS SCHEDULE							
PROFILE							
LABEL ON PLAN	W1	W2	W3	W4	W5		W6
NO'S REQD	2	2	10	36	4		5
DESCRIPTION	Aluminum casement windows with burglary bars, fly and mosquito screen						
DIMENSION (MM)	1800 X 1500	1200 X 1200	600 X 600	750 X 1500	600 X 900	450 X 5400	

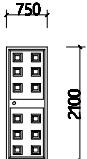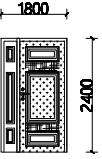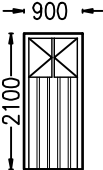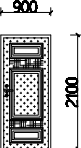DOORS SCHEDULE				
PROFILE				
LABEL ON PLAN	D1	D2	D3	D4
NO'S REQD	10	4	14	3
DESCRIPTION	Single action, single leaf steel panel door with steel frame see manufacturers fixing catalogue for details.	Double action, double leaf steel panel security door with steel frame, see manufacturers fixing catalogue for details.	Single action, single leaf steel panel door with steel frame see manufacturers fixing catalogue for details.	Single action, single leaf steel panel door with steel frame see manufacturers fixing catalogue for details.
DIMENSION (MM)	750 X 2100	1800 X 2400	900 X 2100	900 X 2100

SCHEDULE

NOTE;

general note

- 1) The contractor is to check all the drawing before commencing work.
2) Any discrepancies observed on this drawing issued by any other party are to be immediately brought to consultant Architect Notice.
3) All dimension are in millimeter.
4) Dimension are to be confirmed on site.

Client :-
SURV. SHITTABEY SIRAJDEEN
OLABODE

Location :-
AT AYOBO LOW INCOME RESIDENTIAL
SCHEME, SUBDIVISION OF PLOT 15,
BLOCK 8, AREA (15B)

ALIMOSHO LOCAL AREA, OYOBO,
LAGOS STATE.

Project Title :-

Proposed Residential
Development

Working
Drawing

Architect :-
**YUNGOLA SERVICES
LTD.** RC.1783703
(ARCHITECTURAL DESIGN,
STRUCTURAL DESIGN, BUILDING
DEVELOPMENT, PLANNER,
SUPERVISION
OFFICE ADDRESS:
NO 2 OSHOGBO STREET, OGUDU,
LAGOS STATE
T&L ; 08054178584, 07062539641

Office stamp

sheet content:-
Plan

date :-
MAY, 2024

scale :-
1:100

revision :-


Drawn by :-
Yungola
Checked by :-
Oluwaseun

DETAILS


NOTE;

1	2	3	4	5	6	7	8	9	10
TANK TYPE	NO. of users	per user	total	LENGTH	BREADTH	INLET DEPTH	OUTLET	DEPT. TO Baffle	AVERAGE DEPTH
		cubic meter	cubic meter	A	B	C	D	E	F
A	10	0.197	1.920	2400	800	1275	1200	900	1800
B	15	0.098	1.470	2775	825	1275	1200	1125	1800
C	20	0.084	1.680	3000	1050	1350	1275	1200	1800
D	50	0.070	3.500	3600	1200	1575	1500	1500	1800
E	100	0.070	7.000	4800	1950	1650	1575	2100	1800
F	200	0.070	14.000	6000	2450	1875	1800	2700	1800

TYPICAL SECTION THROUGH LINTEL

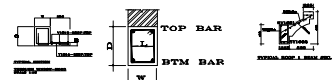


CLEAR SPAN	DEPTH	WIDTH	BTM BARTOP BAR	LINKS
600-1200	225	225	S-Y12 S-Y12	Y10-S200/c
1200-1800	225	225	S-Y12 S-Y12	Y10-S200/c
1800-2400	300	225	S-Y12 S-Y12	Y10-S200/c
2400-3000	300	225	S-Y12 S-Y12	Y10-S200/c


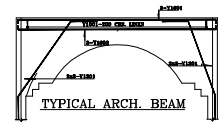


TYPICAL ARCH. SECTION


TYPICAL SOAKWAY AND SEPTIC TANK DETAILS

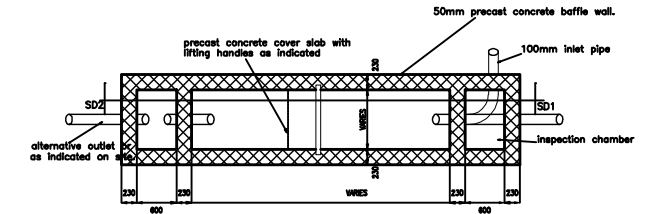







SEPTIC TANK PLAN

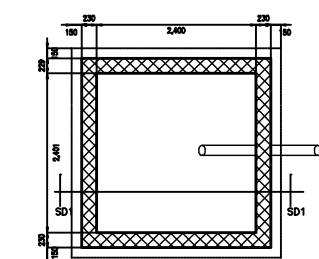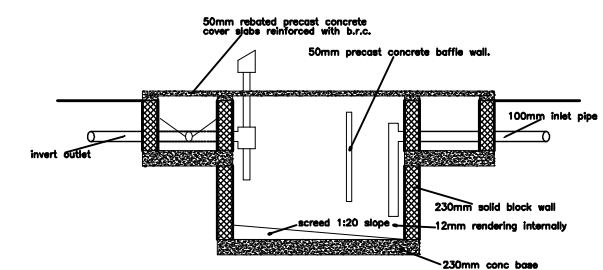

SOAKAWAY (PLAN)

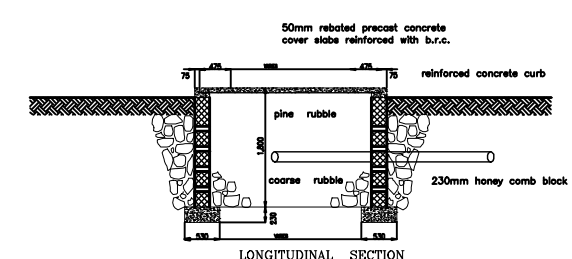

LONGITUDINAL SECTION

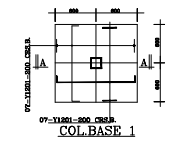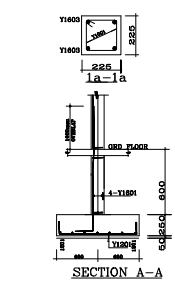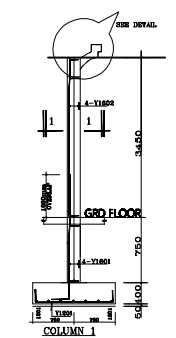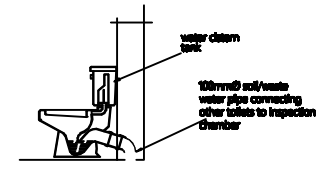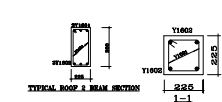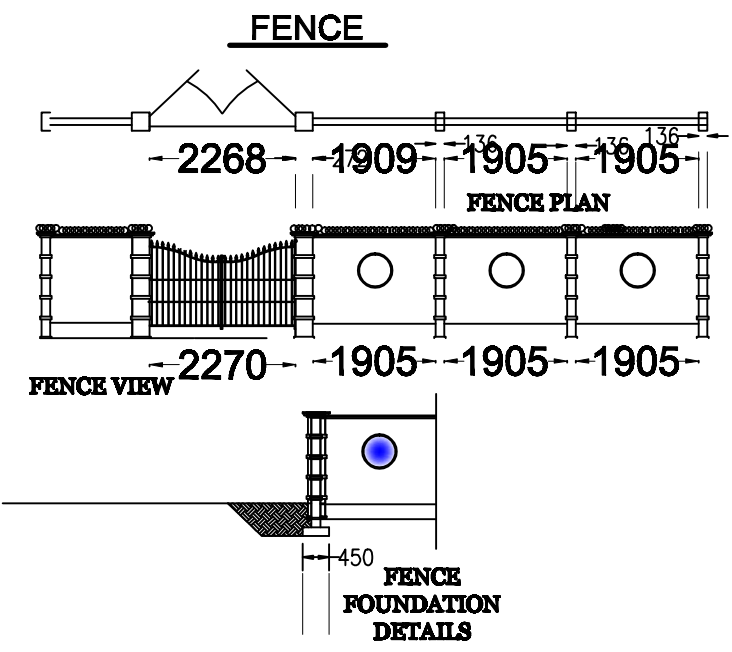

- general note
- 1) The contractor is to check all the drawing before commencing work.
 - 2) Any discrepancies observed on this drawing issued by any other party are to be immediately brought to consultant Architect Notice.
 - 3) All dimension are in millimeter.
 - 4) Dimension are to be confirmed on site.

Client :-
SURV. SHITTABEY SIRAJDEEN
OLABODE

Location :-
AT AYOBO LOW INCOME RESIDENTIAL
SCHEME, SUBDIVI SION OF PLOT 15,
BLOCK 8, AREA (15B)

ALIMOSHO LOCAL AREA, OYOBO,
LAGOS STATE.

Project Title :-

Proposed Residential
Development

Working
Drawing

Architect :-
**YUNGOLA SERVICES
LTD.** Rc.1783703
(ARCHITECTURAL DESIGN,
STRUCTURAL DESIGN, BUILDING
DEVELOPMENT, PLANNER,
SUPERVISION

OFFICE ADDRESS:
NO 2 OSHOGBO STREET, OGUDU,
LAGOS STATE

T&L ; 08054178584, 07062539641

Office stamp

sheet content:-

Plan

scale :-
1:100

date :-
MAY, 2024

revision :-

Drawn by :-
Yungola

Checked by :-
Olurwaserun